


FED. SUP CLASS
1450

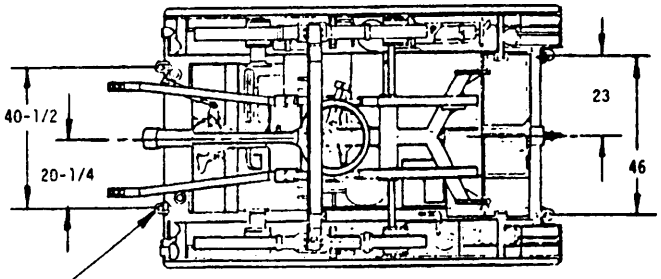



BERNE INTERNATIONAL TUNNEL
OUTLINE STANDARD CAR

VEHICLE SHACKLES, 4 PLACES
CAPACITIES (EACH SHACKLE)
TOWING 6,600 LBS.
TIE DOWN 12,000 LBS.
LIFTING 14,000 LBS.

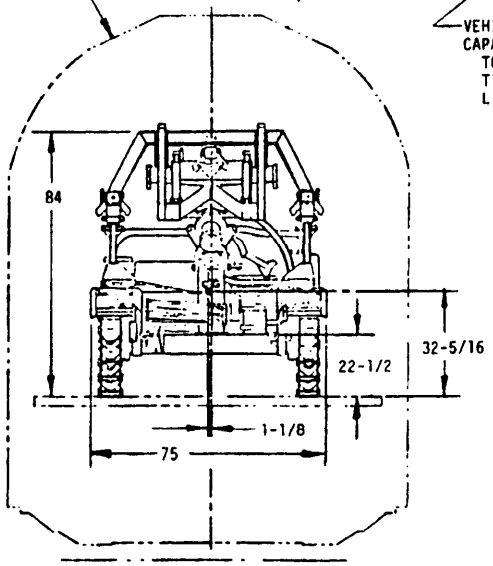

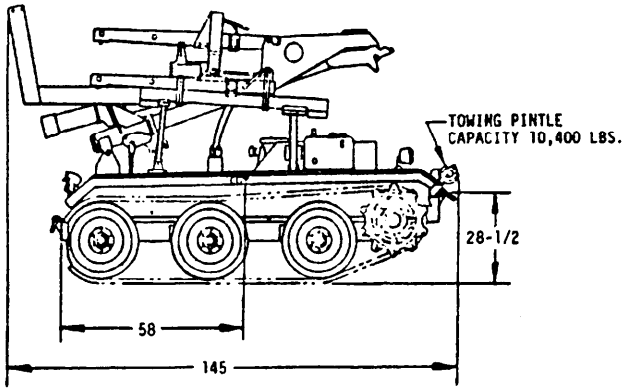

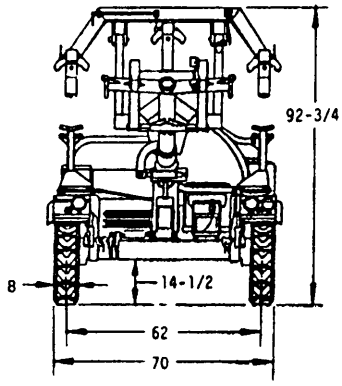

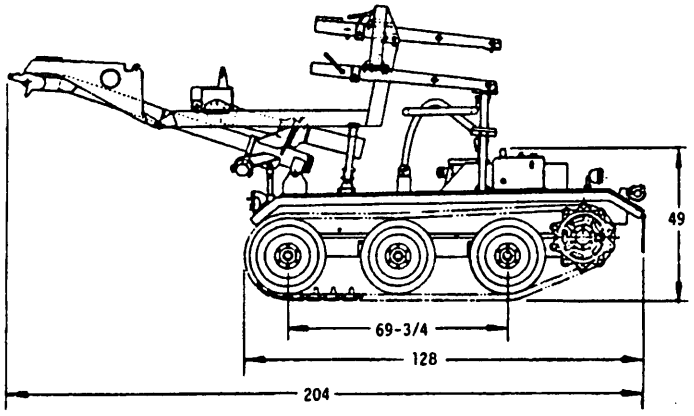

NOTES:
1. DIMENSIONS ARE IN INCHES AND ARE SHOWN FOR ENGINEERING REFERENCE ONLY.
2. REFERENCED DOCUMENTS SHALL BE OF THE ISSUE IN EFFECT ON DATE OF INVITATIONS FOR BID.
3. THIS VEHICLE SHALL BE IN ACCORDANCE WITH REFERENCED ENGINEERING DRAWINGS, COPIES WHICH MAY BE OBTAINED FROM: US ARMY-AUTOMOTIVE COMMAND, WARREN, MICH. 48397-5000.

APPROVED 26 AUG 85 REVISED

MS PART NO.	ENGINEERING DRAWING NO.
MS 52226-1	8750307

P. A. ARMY-AT Other Cust	INTERNATIONAL INTEREST	TITLE LOADER-TRANSPORTER GUIDED MISSILE XM501E3	MILITARY STANDARD MS52226(AT)
PROCUREMENT SPECIFICATION MIL-L-46821	SUPERSEDES:		SHEET 1 OF 2

DD FORM (MAY 73) 672-1 LIMITED COORDINATION

PREVIOUS EDITIONS OF THIS FORM ARE OBSOLETE

This military standard is approved for use by the US Army Tank-Automotive Command, Department of the Army, and is available for use by all Departments and Agencies of the Department of Defense.
DISTRIBUTION STATEMENT A. Approved for public release; distribution is unlimited.

Source: https://assist.dla.mil -- Downloaded: 20260410-23T18:23Z
Check the source to verify that this is the current version before use.

FED. SUP CLASS
1450

VEHICLE CHARACTERSTICS

WEIGHT:
COMBAT LOADED W/PAYLOAD 9513
LESS CREW STOV. & FUEL 5450 LBS
PAYLOAD (3 HAWK MISSILES) 4,194 LBS
UNIT GROUND PRESSURE (W/PAYLAOD)
8.7 LBS/SQ IN

CREW: 1@185 LBS

HYDRAULIC SYSTEM:
NOMINAL OPERATING PRESSURE 3,000 PSI
PUMP: VARIABLE VOLUME, SELF REGULATING, AXIAL PISTON
RATED FLOW: 7.5 GPM@ 3000 RPM

RUNNING GEAR:
SUSPENSION TRAILING ARM TORSION BAR, W/MANUAL LOCKOUT
NO. OF WHEELS 6 DUAL SIZE 23 IN DIA
TRACK CENTER GUIDE, DOUBLE PIN, RUBBERIZED CHEVRON
SHOES/TRACK RH 43 LH 44 SOLID RUBBER
PITCH 6 IN WIDTH 8 IN SIZE 23 X 2

ELECTRICAL SYSTEM: (24 VOLTS)
GENERATOR 25 AMPS 10950808
(2) BATTERY (2HN -12V-45) 20 AMPS MS35000-1
IGNITION SYSTEM (BATTERY)
DISTRIBUTOR NO. 12259526

ENGINE:
CYLINDER IN-LINE
DISPLACEMENT 141.5 CU IN BORE 3.875 IN
STROKE 3.00 IN
GOVERNED SPEED 3800 (REDLINE)
RPM COMPRESSION RATIO 7.50:1
FUEL GASOLINE 80 OCTANE CAP 13 GAL.
MAX. GROSS HORSEPOWER 73 @ 4,200 RPM
MAX. NET HORSEPOWER 62.7 @ 3,600 RPM
MAX. GROSS TORQUE 124.5 LB FT @ 1,800 RPM
MAX. NET TORQUE 118 LB FT @ 1,800 RPM
MAIN COOLING SYS LIQUID
ENG. OIL CAP 4 QTS
OIL COOLING SYSTEM AIR

POWER TRAIN:
HYDRAULIC 3- SPEED AUTOMATIC TRANSMISSION
HYDRAULIC CONVERTER SINGLE STAGE STALL MULTIPLICATION 2.1:1
OVERALL USEABLE RATIO: LOW 41:11 HIGH 16.71 INT 24.39 REV 36.76
TURNING RADIUS 240 IN
STEERING CONTROLLED DIFFERENTIAL MECH, HAND LEVERS (2)
BRAKES WET DRUM TYPE
OIL COOLING SYSTEM AIR

PERFORMANCE:
GROSS HORSEPOWER TO WEIGHT RATIO 15.4 HP/TON
MAX. SPEED (REDLINE) 12.7 MPH MAX. GRADE 40% (W/O LOAD 60%)
MAX. TRENCH 33 IN
MAX. VERTICAL WALL 16 IN
MAX. FORD DEPTH 20 IN
CRUISING RANGE 45 MI
MAX. TRACTIVE EFFORT LOW 11,301 LBS REV 10,105 LBS TE/W LOW 1.187 REV 1.062

FIRE EXTINGUISHER:
FIXED PORTABLE (1) 5 LB CO_2

BASIC LISTS REQUIRED WITH VEHICLE DRAWINGS:
FOR STORAGE AND SHIPMENT MIL-L-45775
TRANSPORTABILITY DATA 10943746
PAINTING PROCEDURE MIL-STD-193

VEHICLE ACCESSORY KITS:
ADAPTER, HOIST 10916330
BEAM, HOISTING XM15 9089788
CRANE, MISSILE LOADER 9098300
RAMP, VEHICLE LOADING (QTY 2) 9008330
KIT, TRACK CLEAT 10943650
KIT, WINTERIZATION +25°F & BELOW 10943820
KIT, WINTERIZATION 0°F TO -65°F 10943830

APPROVED 26 AUG 85 REVISED

MS PART NO.	ENGINEERING DRAWING NO.
MS 52226-1	8750307

P. A. ARMY-AT Other Cust	INTERNATIONAL INTEREST	TITLE LOADER-TRANSPORTER GUIDED MISSILE XM501E3	MILITARY STANDARD MS52226(AT)
PROCUREMENT SPECIFICATION MIL-L-46821	SUPERSEDES:		SHEET 2 OF 2

DD FORM 1 MAY 73 672-1 LIMITED COORDINATION

PREVIOUS EDITIONS OF THIS FORM ARE OBSOLETE

This military standard is approved for use by the US Army Tank-Automotive Command, Department of the Army, and is available for use by all Departments and Agencies of the Department of Defense.
DISTRIBUTION STATEMENT A. Approved for public release; distribution is unlimited.

Source: https://assist.dla.mil -- Downloaded: 2026-10-23T18:23Z
Check the source to verify that this is the current version before use.