(Project No. N5975-N313)

FED. SUP CLASS
5975

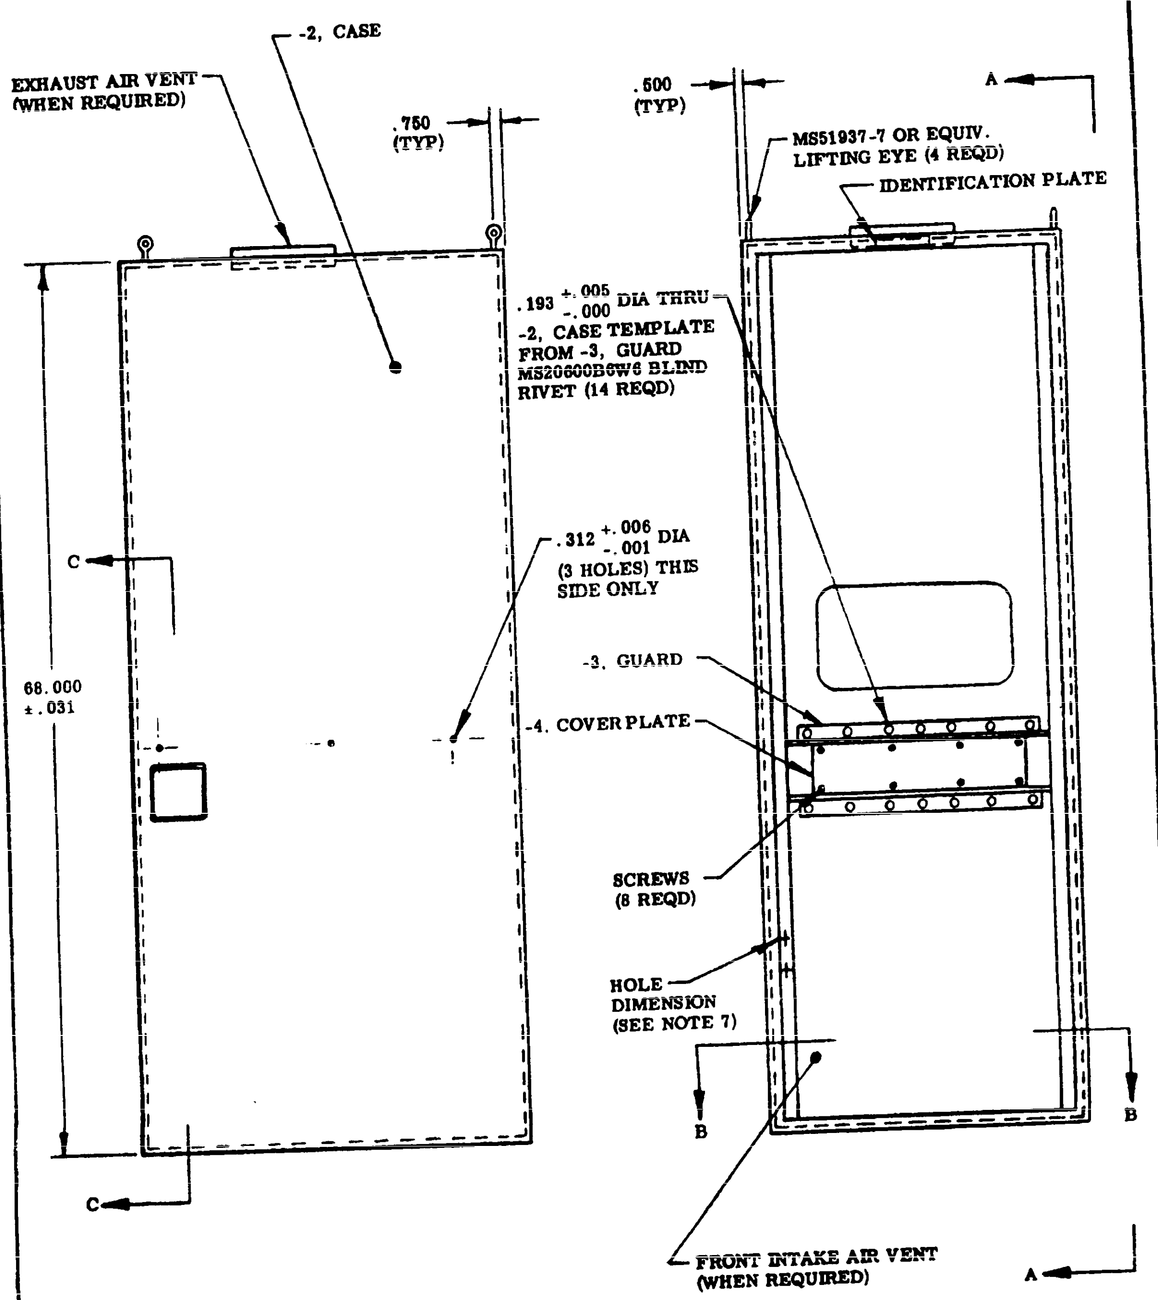
-2, CASE
EXHAUST AIR VENT (WHEN REQUIRED)
.750 (TYP)
.500 (TYP)
A
MS51937-7 OR EQUIV. LIFTING EYE (4 REQD)
IDENTIFICATION PLATE
.193 +.005 -.000 DIA THRU -2, CASE TEMPLATE FROM -3, GUARD MS20600B6W6 BLIND RIVET (14 REQD)
C
.312 +.006 -.001 DIA (3 HOLES) THIS SIDE ONLY
68.000 ±.031
-3, GUARD
-4, COVER PLATE
SCREWS (8 REQD)
HOLE DIMENSION (SEE NOTE 7)
B
B
C
FRONT INTAKE AIR VENT (WHEN REQUIRED)
A

REVISED

APPROVED 24 Mar 70

-1, ASSEMBLY

(FOR NOTES SEE SHEET 5)

This military standard is approved by Naval Air Systems Command, Department of the Navy and is mandatory for use by that activity. All other military activities are required to employ this standard where suitable.

P.A. NAVY - AS Other Cust	TITLE RACK, MODULE, TEST EQUIPMENT	MILITARY STANDARD MS3503(AS)
PROCUREMENT SPECIFICATION	SUPERSEDES:	SHEET 1 OF 6

PLATE NO. 17709

DD FORM 672-1

(Project No. N5975-N313)

FED. SUP CLASS
5975

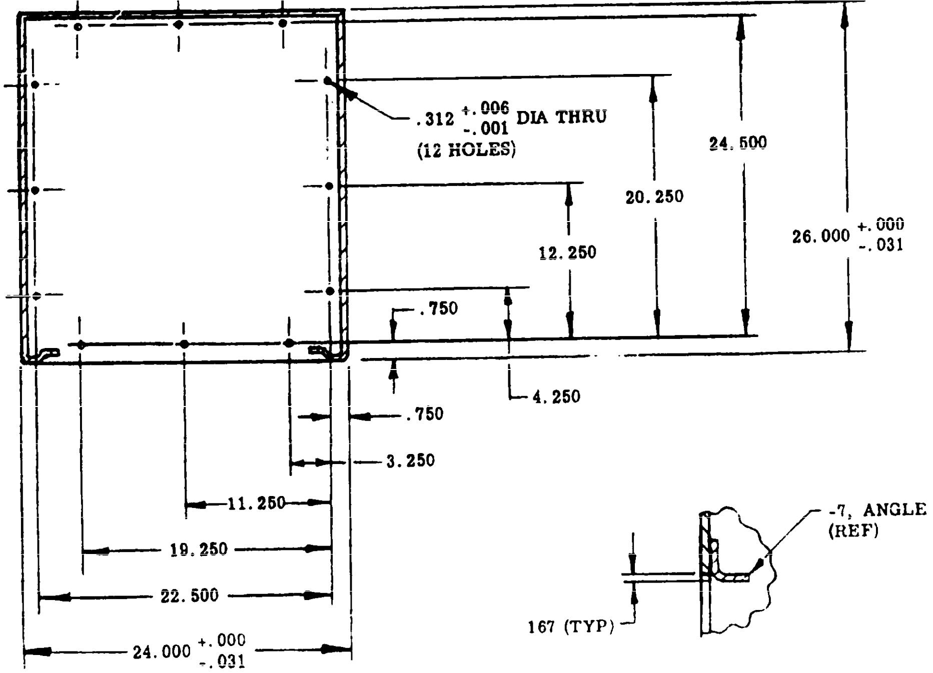

SECTION B-B

SECTION D-D

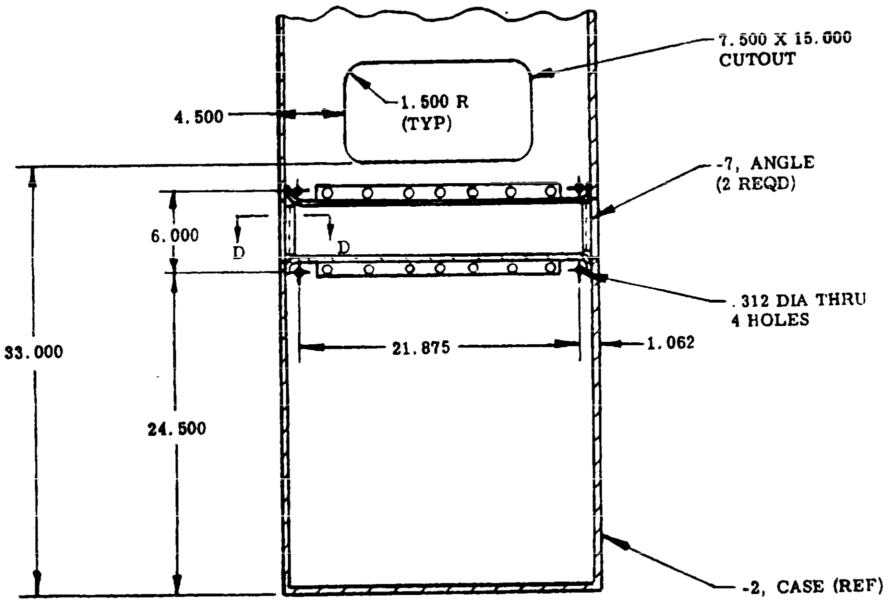

SECTION C-C

This military standard is approved by NAVAL AIR SYSTEMS COMMAND, Department of the Navy and is mandatory for use by that activity. All other military activities are required to employ this standard where suitable.

APPROVED 24 Mar 70 REVISED

P.A. NAVY - AS
Other Cust

TITLE
RACK, MODULE, TEST EQUIPMENT

MILITARY STANDARD
MS3503(AS)

PROCUREMENT SPECIFICATION

SUPERSEDES:

SHEET 2

PLATE NO. 17708

DD FORM 1 OCT 67 672-1 (Limited coordination)

PREVIOUS EDITIONS OF THIS FORM ARE OBSOLETE.

(Project No. N5975-N313)

FED. SUP CLASS
5975

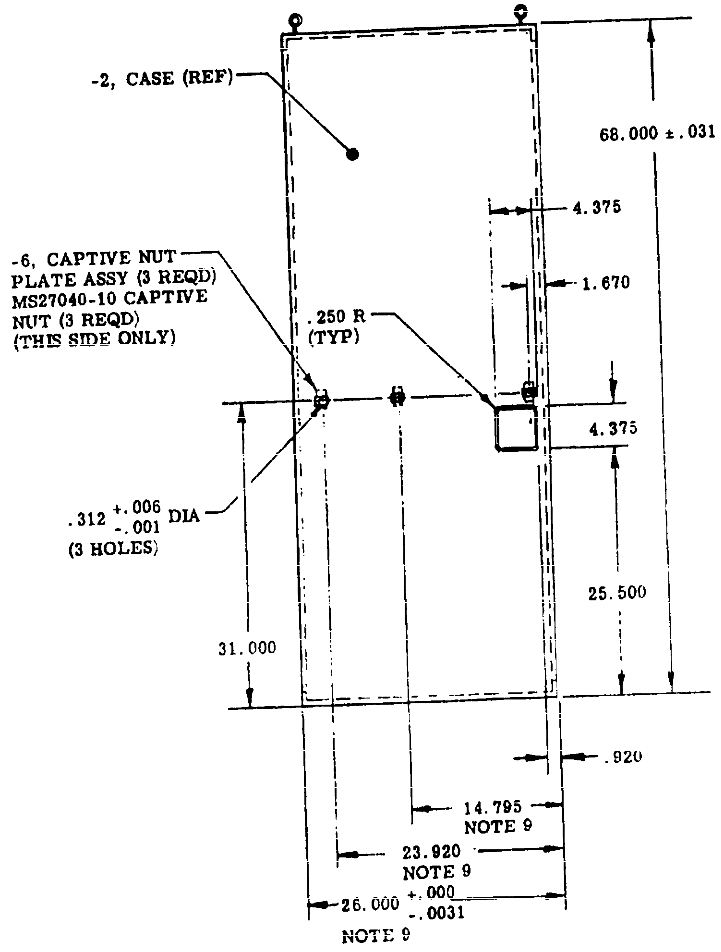
-2, CASE (REF)
68.000 ±.031
4.375
1.670
-6, CAPTIVE NUT PLATE ASSY (3 REQD) MS27040-10 CAPTIVE NUT (3 REQD) (THIS SIDE ONLY)
.250 R (TYP)
4.375
.312 +.006 -.001 DIA (3 HOLES)
25.500
31.000
.920
14.795 NOTE 9
23.920 NOTE 9
26.000 +.000 -.0031 NOTE 9

VIEW A-A

HOLE AND OPENING DIMENSIONS ARE TYPICAL FOR RIGHT AND LEFT HAND SIDES

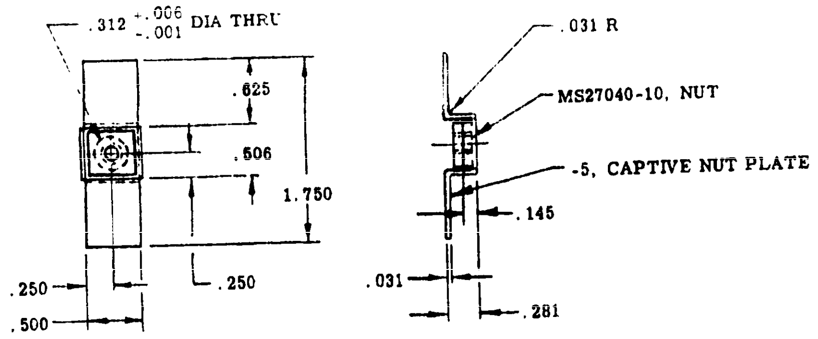

-6, CAPTIVE NUT PLATE ASSEMBLY

This military standard is approved by NAVAL AIR SYSTEMS COMMAND, Department of the Navy and is mandatory for use by that activity. All other military activities are required to employ this standard where suitable.

APPROVED 24 Mar 70 REVISED

P.A. NAVY - AS Other Cust	TITLE RACK, MODULE, TEST EQUIPMENT	MILITARY STANDARD MS3503(AS)
PROCUREMENT SPECIFICATION	SUPERSEDES:	SHEET 3

PLATE NO. 17709

DD FORM 1 SEP 67 672-1 (Limited coordination) PREVIOUS EDITIONS OF THIS FORM ARE OBSOLETE.

(Project No. N5975-N313)

FED. SUP CLASS
5975

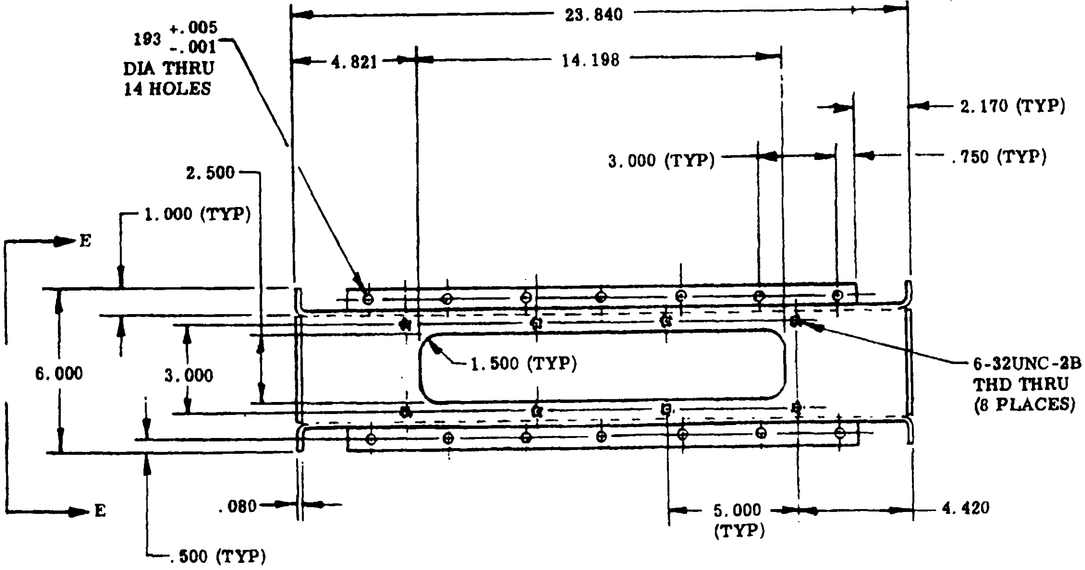

-3, GUARD

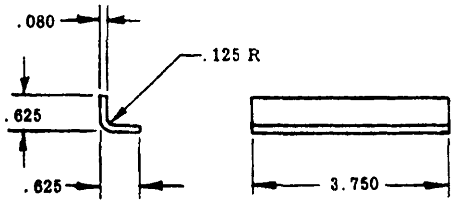

-7, ANGLE

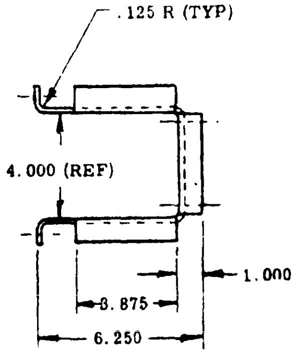

VIEW E-E

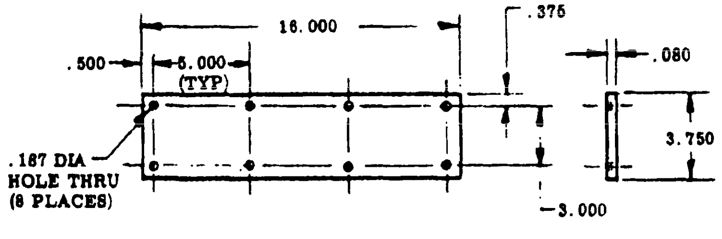

-4, COVER PLATE

APPROVED 24 Mar 70 REVISED

This military standard is approved by NAVAL AIR SYSTEMS COMMAND, Department of the Navy and is mandatory for use by that activity. All other military activities are required to employ this standard where suitable.

P.A. NAVY - AS Other Cust	TITLE RACK, MODULE, TEST EQUIPMENT	**MILITARY STANDARD** **MS3503(AS)**
PROCUREMENT SPECIFICATION	SUPERSEDES:	SHEET 4

DD FORM 1 SEP 67 672-1 *(Limited coordination)*

PREVIOUS EDITIONS OF THIS FORM ARE OBSOLETE.

PLATE NO. 17709

(Project No. N5975-N313)

FED. SUP CLASS
5975

NOTES:

1. MATERIAL: CASE, -2, GUARD, -3, COVER PLATE, -4, AND CAPTIVE NUT PLATE, -5 AND ANGLE, -7, ALUMINUM ALLOY, QQ-A-250/8 (H32).
2. FINISH: CASE, -2, GUARD, -3, COVER PLATE, -4 AND CAPTIVE NUT PLATE, -5, AND ANGLE, -7, ONE PRIME COAT OF FORMULA 117 OR 126 AND ONE COAT OF FORMULA 111, MIL-F-902.
3. ALL ALUMINUM ALLOY PARTS SHALL BE CLEANED BEFORE ASSEMBLY OR PAINTING IN ACCORDANCE WITH 5.1.3.4 OF MIL-STD-171.
4. ALL RIVETS SHALL BE ALUMINUM ALLOY CONFORMING TO MS20470 OR MS20426 AS APPROPRIATE.
5. REMOVE ALL BURRS AND BREAK ALL SHARP EDGES.
6. DIMENSIONS IN INCHES. UNLESS OTHERWISE SPECIFIED, TOLERANCES: DECIMALS ±.015. TOLERANCE FOR MOUNTING HOLE LOCATION OF COVER PLATE, -4, SHALL BE ±.010.
7. RACK PANEL MOUNTING HOLES SHALL BE LOCATED IN ACCORDANCE WITH MIL-STD-189, TABLE II.
8. UNLESS OTHERWISE SPECIFIED ALL RADII SHALL BE .062 MAX. RADII FOR .080 THICK ALUMINUM SHALL BE .031 MAX.
9. HOLES INDICATED ⌖ SHALL BE LOCATED AT TRUE POSITION WITHIN .010 INCH.
10. MAXIMUM WEIGHT INCLUDING INSTALLED EQUIPMENT SHALL BE 1200 LBS.
11. THREADS SHALL CONFORM TO HANDBOOK H28.

FOR DESIGN FEATURE PURPOSES, THIS STANDARD TAKES PRECEDENCE OVER PROCUREMENT DOCUMENTS REFERENCED HEREIN. REFERENCED DOCUMENTS SHALL BE OF THE ISSUE IN EFFECT ON DATE OF INVITATIONS FOR BID

APPROVED 24 Mar 70 REVISED

This military standard is approved by NAVAL AIR SYSTEMS COMMAND, Department of the Navy and is mandatory for use by that activity. All other military activities are required to employ this standard when suitable.

P.A NAVY – AS Other Cust	TITLE RACK, MODULE, TEST EQUIPMENT	MILITARY STANDARD MS3503(AS)
PROCUREMENT SPECIFICATION	SUPERSEDES:	SHEET 5

DD FORM 1 SEP 67 672-1 (Limited coordination) PREVIOUS EDITIONS OF THIS FORM ARE OBSOLETE. PLATE NO. 17700

This military standard is approved by NAVAL AIR SYSTEMS COMMAND, Department of the Navy and is mandatory for use by that activity. All other military activities are required to employ this standard where suitable.

(Project No. N5975-N313)

FED. SUP CLASS
5975

RACK, MODULE
AS INSTALLED
IN
ELECTRONIC
WORKBENCH
ASSEMBLY
63A114 - REV-A
(REFERENCE)

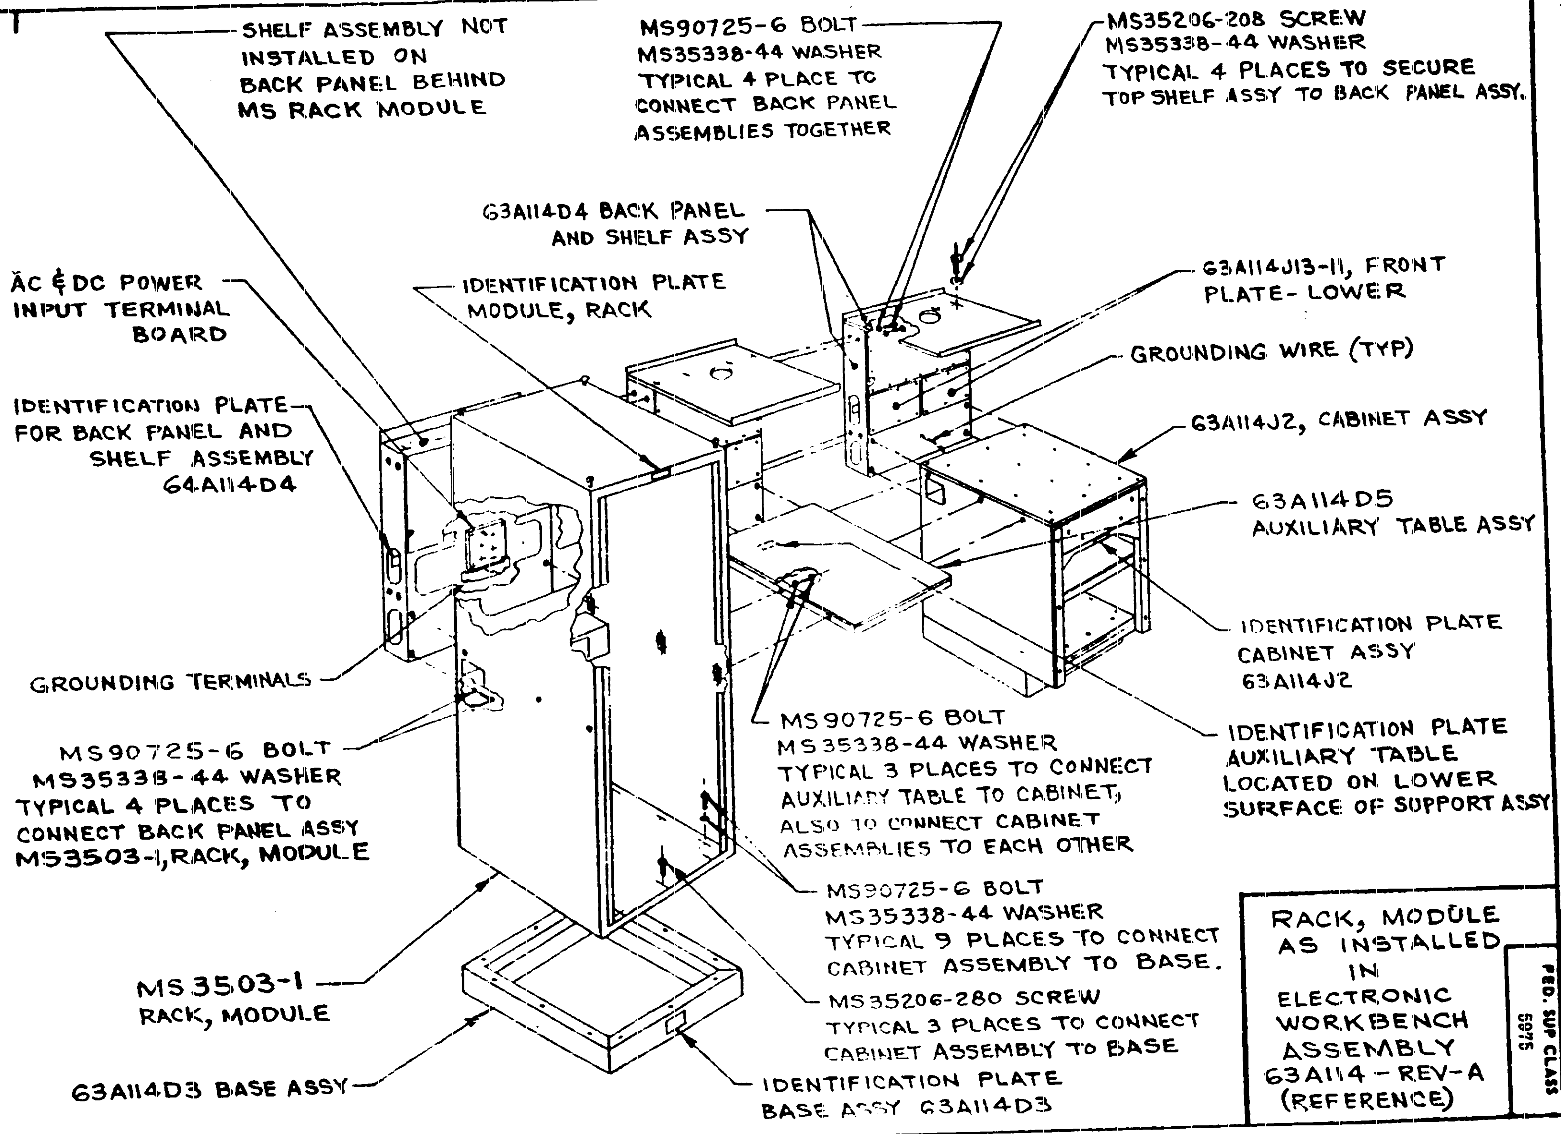
SHELF ASSEMBLY NOT INSTALLED ON BACK PANEL BEHIND MS RACK MODULE
MS90725-6 BOLT MS35338-44 WASHER TYPICAL 4 PLACE TO CONNECT BACK PANEL ASSEMBLIES TOGETHER
MS35206-208 SCREW MS35338-44 WASHER TYPICAL 4 PLACES TO SECURE TOP SHELF ASSY TO BACK PANEL ASSY.
63A114D4 BACK PANEL AND SHELF ASSY
AC & DC POWER INPUT TERMINAL BOARD
IDENTIFICATION PLATE MODULE, RACK
63A114J13-11, FRONT PLATE- LOWER
GROUNDING WIRE (TYP)
IDENTIFICATION PLATE FOR BACK PANEL AND SHELF ASSEMBLY 64A114D4
63A114J2, CABINET ASSY
63A114D5 AUXILIARY TABLE ASSY
IDENTIFICATION PLATE CABINET ASSY 63A114J2
GROUNDING TERMINALS
MS90725-6 BOLT MS35338-44 WASHER TYPICAL 3 PLACES TO CONNECT AUXILIARY TABLE TO CABINET, ALSO TO CONNECT CABINET ASSEMBLIES TO EACH OTHER
IDENTIFICATION PLATE AUXILIARY TABLE LOCATED ON LOWER SURFACE OF SUPPORT ASSY
MS90725-6 BOLT MS35338-44 WASHER TYPICAL 4 PLACES TO CONNECT BACK PANEL ASSY MS3503-1, RACK, MODULE
MS90725-6 BOLT MS35338-44 WASHER TYPICAL 9 PLACES TO CONNECT CABINET ASSEMBLY TO BASE.
MS3503-1 RACK, MODULE
MS35206-280 SCREW TYPICAL 3 PLACES TO CONNECT CABINET ASSEMBLY TO BASE
63A114D3 BASE ASSY
IDENTIFICATION PLATE BASE ASSY 63A114D3

APPROVED 24 Mar 70 REVISED

F.A. NAVY - AS Other Cust	TITLE RACK, MODULE, TEST EQUIPMENT	MILITARY STANDARD MS3503(AS)
PROCUREMENT SPECIFICATION	SUPERSEDES:	SHEET 6

PLATE NO. 17709

DD FORM 1 SEP 57 672-1 (Limited coordination)

PREVIOUS EDITIONS OF THIS FORM ARE OBSOLETE.