
Form approved
OMB No. 0704-0188

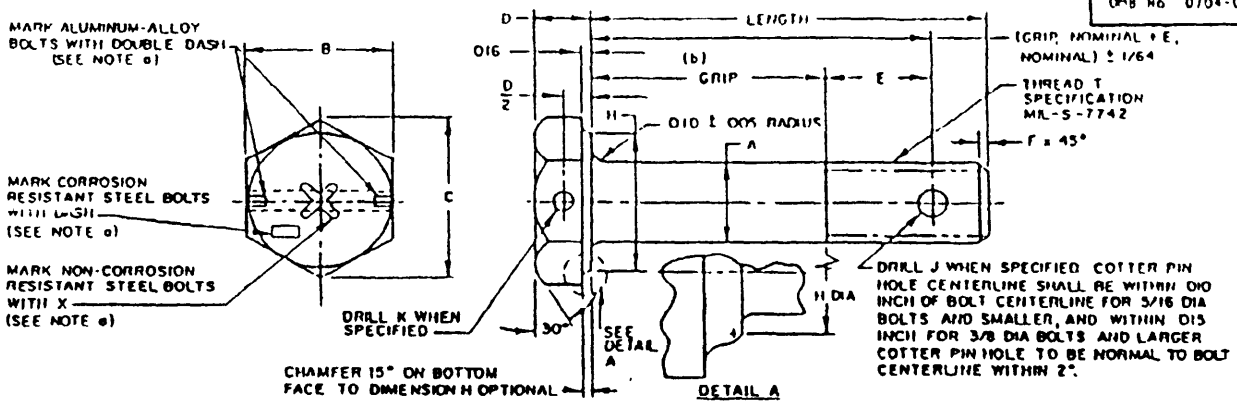

BASIC AN PART NO	THREAD T	A DIA MAX	A DIA MIN	B MAX	B MIN	C REF	D MAX	D MIN	E REF	F MAX	F MIN	H DIA MIN	J DRILL +.010 -.000	K DRILL +.010 -.000
AN3	NO. 10-32 UNF-3A	.189	.186	.377	.365	.430	.141	.109	17/64	.047	.015	.335	.070	.046
AN4	1/4 -28 UNF-3A	.249	.246	.440	.428	.510	.172	.140	5/16	.047	.015	.398	.076	.046
AN5	5/16-24 UNF-3A	.312	.309	.502	.490	.580	.204	.172	23/64	.063	.031	.460	.076	.070
AN6	3/8 -24 UNF-3A	.374	.371	.565	.553	.650	.235	.203	7/16		.031	.523	.106	.070
AN7	7/16-20 UNF-3A	.437	.433	.627	.615	.720	.266	.234	31/64	.063	.031	.585	.106	.070
AN8	1/2 -20 UNF-3A	.499	.495	.752	.740	.870	.297	.265	39/64		.031	.710	.106	.070
AN9	9/16-18 UNF-3A	.562	.558	.877	.865	1.010	.328	.296	21/32		.046	.835	.141	.070
AN10	5/8 -18 UNF-3A	.624	.620	.940	.928	1.090	.360	.328	47/64	.078	.046	.898	.141	.070
AN12	3/4 -16 UNF-3A	.749	.744	1.066	1.053	1.230	.422	.390	7/8		.046	1.023	.141	.070
AN14	7/8 -14 UNF-3A	.874	.869	1.253	1.240	1.440	.485	.453	63/64		.062	1.210	.141	.070
(12) (d) AN16	1 -14 NF-3A	.999	.993	1.441	1.428	1.660	.547	.515	1-3/32	.094	.062	1.398	.141	.070
AN17	1 -12 UNF-3A	.999	.993	1.441	1.428	1.660	.547	.515	1-3/32	.094	.062	1.398	.141	.070
AN18	1-1/8 -12 UNF-3A	1.124	1.118	1.628	1.615	1.880	.610	.578	1-3/16		.078	1.585	.141	.070
AN20	1-1/4 -12 UNF-3A	1.249	1.243	1.815	1.802	2.090	.672	.640	1-3/8	.110	.078	1.772	.141	.070

SEE SHEET 3 FOR NOTE (b).

(a) MARKING MAY BE EITHER RAISED OR DEPRESSED. THE HEIGHT OR DEPTH OF THE MARKINGS SHALL NOT EXCEED THE FOLLOWING VALUES: .025 INCH FOR 9/16 DIAMETER BOLTS AND SMALLER; .030 INCH FOR 5/8 DIAMETER BOLTS AND LARGER. HEAD MARKING MAY INCLUDE MANUFACTURER'S MARKINGS.
(c) THE DIAMETER OF THE WASHER FACE SHALL NOT EXCEED THE ACTUAL WIDTH ACROSS FLATS.
(d) 1-14NF THREAD PITCH INACTIVE FOR DESIGN AFTER 15 JUNE 1966.

MATERIAL: NON-CORROSION RESISTANT STEEL, CORROSION-RESISTANT STEEL OR ALUMINUM ALLOY. SEE PROCUREMENT SPECIFICATION.
FINISH: SEE PROCUREMENT SPECIFICATION.

(12) ADD "C" BEFORE DASH NUMBER FOR CORROSION-RESISTANT STEEL BOLT.
ADD "D" BEFORE DASH NUMBER FOR ALUMINUM ALLOY BOLT.
ADD "A" AFTER DASH NUMBER FOR UNDRILLED BOLT. SEE ILLUSTRATION.
ADD "H" BEFORE DASH NUMBER FOR BOLT WITH DRILLED HEAD AND SHANK. SEE ILLUSTRATION.
ADD "H" BEFORE DASH NUMBER AND "A" AFTER DASH NUMBER FOR BOLT WITH DRILLED HEAD ONLY. SEE ILLUSTRATION.

EXAMPLES OF PART NUMBERS:
AN6-10 = 3/8 NON-CORROSION RESISTANT STEEL BOLT 1-5/64 LONG, 7/16 GRIP WITH DRILLED SHANK ONLY. SEE ILLUSTRATION.
AN6C10 = 3/8 CORROSION-RESISTANT STEEL BOLT 1-5/64 LONG, 7/16 GRIP WITH DRILLED SHANK ONLY. SEE ILLUSTRATION.
AN6D10 = 3/8 ALUMINUM ALLOY BOLT 1-5/64 LONG, 7/16 GRIP WITH DRILLED SHANK ONLY. SEE ILLUSTRATION.
AN6D10A = 3/8 ALUMINUM ALLOY BOLT 1-5/64 LONG, 7/16 GRIP, UNDRILLED SHANK AND HEAD. SEE ILLUSTRATION.
AN6DH10 = 3/8 ALUMINUM ALLOY BOLT 1-5/64 LONG, 7/16 GRIP WITH DRILLED HEAD AND SHANK. SEE ILLUSTRATION.
AN6DH10A = 3/8 ALUMINUM ALLOY BOLT 1-5/64 LONG, 7/16 GRIP WITH DRILLED HEAD ONLY. SEE ILLUSTRATION.

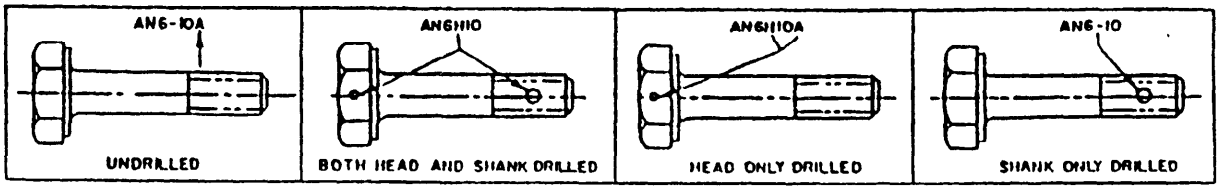


ILLUSTRATION OF DRILLED AND UNDRILLED BOLTS AND PART NUMBERS

BOLTS SHALL BE FREE FROM ALL HANGING BURRS AND SLIVERS WHICH MIGHT BECOME DISLODGED UNDER USAGE. COUNTERSINKING OF DRILLED HOLES IN HEAD IS MANDATORY. COUNTERSINKING OF DRILLED HOLES IN SHANK IS OPTIONAL.

DIMENSIONS ARE IN INCHES. UNLESS OTHERWISE SPECIFIED, TOLERANCES: DECIMALS ±.010, ANGLES ±5°.

(12) FOR CHANGES SEE SHEETS 1 AND 2

PREPARING ACTIVITY NAVY - AS	MILITARY SPECIFICATION SHEET	SPECIFICATION SHEET NUMBER
CUSTODIANS ARMY - AV NAVY - AS AIR FORCE - 99 DLA - IS	TITLE BOLT - MACHINE, AIRCRAFT	AN3 THRU AN20 14 JAN 91 (12)
REVIEW USER		SUPERSEDING AN3 THRU AN20 26 FEB 1990
PROJECT NUMBER 5306-1415		AMSC- N/A FSC 5306

DISTRIBUTION STATEMENT A. Approved for public release, distribution is unlimited

DD FORM 672 MAY 1988 PREVIOUS EDITIONS OF THIS FORM ARE OBSOLETE

THE REQUIREMENTS FOR ACQUIRING THE PRODUCT(S) DESCRIBED HEREIN SHALL CONSIST OF THIS SPECIFICATION SHEET AND THE ISSUE OF THE FOLLOWING SPECIFICATION LISTED IN THAT ISSUE OF THE DODISS SPECIFIED IN THE SOLICITATION: MIL-B-8942

THIS SPECIFICATION IS APPROVED FOR USE BY ALL DEPARTMENTS AND AGENCIES OF THE DEPARTMENT OF DEFENSE.

Source: https://assist.dla.mil -- Downloaded: 2026-10-26T14:14Z
Check the source to verify that this is the current version before use.

Form approved
OMB No 0704-0188

(12)

DASH NO	AN3 GRIP ±1/64	AN3 LENGTH +1/32 -1/64	AN4 GRIP ±1/64	AN4 LENGTH +1/32 -1/64	AN5 GRIP ±1/64	AN5 LENGTH +1/32 -1/64	AN6 GRIP +1/64	AN6 LENGTH -1/32 -1/64	AN7 GRIP -1/64	AN7 LENGTH +1/32 -1/64	AN8 GRIP ±1/64	AN8 LENGTH +1/32 -1/64	AN9 GRIP ±1/64	AN9 LENGTH +1/32 -1/64
3	1/16	15/32	1/16	15/32										
4	1/8	17/32	1/16	17/32	1/16	19/32								
5	1/4	21/32	3/16	21/32	3/16	23/32	1/16	45/64	1/16	23/32				
6	3/8	25/32	5/16	25/32	5/16	27/32	3/16	53/64	3/16	27/32	1/16	27/32	1/16	31/32
7	1/2	29/32	7/16	29/32	7/16	31/32	5/16	61/64	5/16	31/32	3/16	31/32	1/8	1- 1/32
10	5/8	1- 1/32	9/16	1- 1/32	9/16	1- 3/32	7/16	1- 5/64	7/16	1- 3/32	5/16	1- 3/32	1/4	1- 5/32
11	3/4	1- 5/32	11/16	1- 5/32	11/16	1- 7/32	9/16	1-13/64	9/16	1- 7/32	7/16	1- 7/32	3/8	1- 9/32
12	7/8	1- 9/32	13/16	1- 9/32	13/16	1-11/32	11/16	1-21/64	11/16	1-11/32	9/16	1-11/32	1/2	1-13/32
13	1	1-13/32	15/16	1-13/32	15/16	1-15/32	13/16	1-29/64	13/16	1-15/32	11/16	1-15/32	5/8	1-17/32
14	1-1/8	1-17/32	1- 1/16	1-17/32	1- 1/16	1-19/32	15/16	1-37/64	15/16	1-19/32	13/16	1-19/32	3/4	1-21/32
15	1-1/4	1-21/32	1- 3/16	1-21/32	1- 3/16	1-23/32	1- 1/16	1-45/64	1- 1/16	1-23/32	15/16	1-23/32	7/8	1-25/32
16	1-3/8	1-25/32	1- 5/16	1-25/32	1- 5/16	1-27/32	1- 3/16	1-53/64	1- 3/16	1-27/32	1-1/16	1-27/32	1	1-29/32
17	1-1/2	1-29/32	1- 7/16	1-29/32	1- 7/16	1-31/32	1- 5/16	1-61/64	1- 5/16	1-31/32	1- 3/16	1-31/32	1-1/8	2- 1/32
20	1-5/8	2- 1/32	1- 9/16	2- 1/32	1- 9/16	2- 3/32	1- 7/16	2- 5/64	1- 7/16	2- 3/32	1- 5/16	2- 3/32	1-1/4	2- 5/32
21	1-3/4	2- 5/32	1-11/16	2- 5/32	1-11/16	2- 7/32	1- 9/16	2-13/64	1- 9/16	2- 7/32	1- 7/16	2- 7/32	1-3/8	2- 9/32
22	1-7/8	2- 9/32	1-13/16	2- 9/32	1-13/16	2-11/32	1-11/16	2-21/64	1-11/16	2-11/32	1- 9/16	2-11/32	1-1/2	2-13/32
23	2	2-13/32	1-15/16	2-13/32	1-15/16	2-15/32	1-13/16	2-29/64	1-13/16	2-15/32	1-11/16	2-15/32	1-5/8	2-17/32
24	2-1/8	2-17/32	2- 1/16	2-17/32	2- 1/16	2-19/32	1-15/16	2-37/64	1-15/16	2-19/32	1-13/16	2-19/32	1-3/4	2-21/32
25	2-1/4	2-21/32	2- 3/16	2-21/32	2- 3/16	2-23/32	2- 1/16	2-45/64	2- 1/16	2-23/32	1-15/16	2-23/32	1-7/8	2-25/32
26	2-3/8	2-25/32	2- 5/16	2-25/32	2- 5/16	2-27/32	2- 3/16	2-53/64	2- 3/16	2-27/32	2-1/16	2-27/32	2	2-29/32
27	2-1/2	2-29/32	2- 7/16	2-29/32	2- 7/16	2-31/32	2- 5/16	2-61/64	2- 5/16	2-31/32	2-3/16	2-31/32	2-1/8	3- 1/32
30	2-5/8	3- 1/32	2- 9/16	3- 1/32	2- 9/16	3- 3/32	2- 7/16	3- 5/64	2- 7/16	3- 3/32	2-5/16	3- 3/32	2-1/4	3- 5/32
31	2-3/4	3- 5/32	2-11/16	3- 5/32	2-11/16	3- 7/32	2- 9/16	3-13/64	2- 9/16	3- 7/32	2-7/16	3- 7/32	2-3/8	3- 9/32
32	2-7/8	3- 9/32	2-13/16	3- 9/32	2-13/16	3-11/32	2-11/16	3-21/64	2-11/16	3-11/32	2-9/16	3-11/32	2-1/2	3-13/32
33	3	3-13/32	2-15/16	3-13/32	2-15/16	3-15/32	2-13/16	3-29/64	2-13/16	3-15/32	2-11/16	3-15/32	2-5/8	3-17/32
34	3-1/8	3-17/32	3- 1/16	3-17/32	3- 1/16	3-19/32	2-15/16	3-37/64	2-15/16	3-19/32	2-13/16	3-19/32	2-3/4	3-21/32
35	3-1/4	3-21/32	3- 3/16	3-21/32	3- 3/16	3-23/32	3- 1/16	3-45/64	3- 1/16	3-23/32	2-15/16	3-23/32	2-7/8	3-25/32
36	3-3/8	3-25/32	3- 5/16	3-25/32	3- 5/16	3-27/32	3- 3/16	3-53/64	3- 3/16	3-27/32	3-1/16	3-27/32	3	3-29/32
37	3-1/2	3-29/32	3- 7/16	3-29/32	3- 7/16	3-31/32	3- 5/16	3-61/64	3- 5/16	3-31/32	3-3/16	3-31/32	3-1/8	4- 1/32
40	3-5/8	4- 1/32	3- 9/16	4- 1/32	3- 9/16	4- 3/32	3- 7/16	4- 5/64	3- 7/16	4- 3/32	3-5/16	4- 3/32	3-1/4	4- 5/32
41	3-3/4	4- 5/32	3-11/16	4- 5/32	3-11/16	4- 7/32	3- 9/16	4-13/64	3- 9/16	4- 7/32	3-7/16	4- 7/32	3-3/8	4- 9/32
42	3-7/8	4- 9/32	3-13/16	4- 9/32	3-13/16	4-11/32	3-11/16	4-21/64	3-11/16	4-11/32	3-9/16	4-11/32	3-1/2	4-13/32
43	4	4-13/32	3-15/16	4-13/32	3-15/16	4-15/32	3-13/16	4-29/64	3-13/16	4-15/32	3-11/16	4-15/32	3-5/8	4-17/32
44	4-1/8	4-17/32	4- 1/16	4-17/32	4- 1/16	4-19/32	3-15/16	4-37/64	3-15/16	4-19/32	3-13/16	4-19/32	3-3/4	4-21/32
45	4-1/4	4-21/32	4- 3/16	4-21/32	4- 3/16	4-23/32	4- 1/16	4-45/64	4- 1/16	4-23/32	3-15/16	4-23/32	3-7/8	4-25/32
46	4-3/8	4-25/32	4- 5/16	4-25/32	4- 5/16	4-27/32	4- 3/16	4-53/64	4- 3/16	4-27/32	4-1/16	4-27/32	4	4-29/32
47	4-1/2	4-29/32	4- 7/16	4-29/32	4- 7/16	4-31/32	4- 5/16	4-61/64	4- 5/16	4-31/32	4-3/16	4-31/32	4-1/8	5- 1/32
50	4-5/8	5- 1/32	4- 9/16	5- 1/32	4- 9/16	5- 3/32	4- 7/16	5- 5/64	4- 7/16	5- 3/32	4-5/16	5- 3/32	4-1/4	5- 5/32
51	4-3/4	5- 5/32	4-11/16	5- 5/32	4-11/16	5- 7/32	4- 9/16	5-13/64	4- 9/16	5- 7/32	4-7/16	5- 7/32	4-3/8	5- 9/32
52	4-7/8	5- 9/32	4-13/16	5- 9/32	4-13/16	5-11/32	4-11/16	5-21/64	4-11/16	5-11/32	4-9/16	5-11/32	4-1/2	5-13/32
53	5	5-13/32	4-15/16	5-13/32	4-15/16	5-15/32	4-13/16	5-29/64	4-13/16	5-15/32	4-11/16	5-15/32	4-5/8	5-17/32
54	5-1/8	5-17/32	5- 1/16	5-17/32	5- 1/16	5-19/32	4-15/16	5-37/64	4-15/16	5-19/32	4-13/16	5-19/32	4-3/4	5-21/32
55	5-1/4	5-21/32	5- 3/16	5-21/32	5- 3/16	5-23/32	5- 1/16	5-45/64	5- 1/16	5-23/32	4-15/16	5-23/32	4-7/8	5-25/32
56	5-3/8	5-25/32	5- 5/16	5-25/32	5- 5/16	5-27/32	5- 3/16	5-53/64	5- 3/16	5-27/32	5-1/16	5-27/32	5	5-29/32
57	5-1/2	5-29/32	5- 7/16	5-29/32	5- 7/16	5-31/32	5- 5/16	5-61/64	5- 5/16	5-31/32	5-3/16	5-31/32	5-1/8	6- 1/32
60	5-5/8	6- 1/32	5- 9/16	6- 1/32	5- 9/16	6- 3/32	5- 7/16	6- 5/64	5- 7/16	6- 3/32	5-5/16	6- 3/32	5-1/4	6- 5/32
61	5-3/4	6- 5/32	5-11/16	6- 5/32	5-11/16	6- 7/32	5- 9/16	6-13/64	5- 9/16	6- 7/32	5-7/16	6- 7/32	5-3/8	6- 9/32
62	5-7/8	6- 9/32	5-13/16	6- 9/32	5-13/16	6-11/32	5-11/16	6-21/64	5-11/16	6-11/32	5-9/16	6-11/32	5-1/2	6-13/32
63	6	6-13/32	5-15/16	6-13/32	5-15/16	6-15/32	5-13/16	6-29/64	5-13/16	6-15/32	5-11/16	6-15/32	5-5/8	6-17/32
64	6-1/8	6-17/32	6- 1/16	6-17/32	6- 1/16	6-19/32	5-15/16	6-37/64	5-15/16	6-19/32	5-13/16	6-19/32	5-3/4	6-21/32
65	6-1/4	6-21/32	6- 3/16	6-21/32	6- 3/16	6-23/32	6- 1/16	6-45/64	6- 1/16	6-23/32	5-15/16	6-23/32	5-7/8	6-25/32
66	6-3/8	6-25/32	6- 5/16	6-25/32	6- 5/16	6-27/32	6- 3/16	6-53/64	6- 3/16	6-27/32	6-1/16	6-27/32	6	6-29/32
67	6-1/2	6-29/32	6- 7/16	6-29/32	6- 7/16	6-31/32	6- 5/16	6-61/64	6- 5/16	6-31/32	6-3/16	6-31/32	6-1/8	7- 1/32
70	6-5/8	7- 1/32	6- 9/16	7- 1/32	6- 9/16	7- 3/32	6- 7/16	7- 5/64	6- 7/16	7- 3/32	6-5/16	7- 3/32	6-1/4	7- 5/32
71	6-3/4	7- 5/32	6-11/16	7- 5/32	6-11/16	7- 7/32	6- 9/16	7-13/64	6- 9/16	7- 7/32	6-7/16	7- 7/32	6-3/8	7- 9/32
72	6-7/8	7- 9/32	6-13/16	7- 9/32	6-13/16	7-11/32	6-11/16	7-21/64	6-11/16	7-11/32	6-9/16	7-11/32	6-1/2	7-13/32
73	7	7-13/32	6-15/16	7-13/32	6-15/16	7-15/32	6-13/16	7-29/64	6-13/16	7-15/32	6-11/16	7-15/32	6-5/8	7-17/32
74	7-1/8	7-17/32	7- 1/16	7-17/32	7- 1/16	7-19/32	6-15/16	7-37/64	6-15/16	7-19/32	6-13/16	7-19/32	6-3/4	7-21/32
75	7-1/4	7-21/32	7- 3/16	7-21/32	7- 3/16	7-23/32	7- 1/16	7-45/64	7- 1/16	7-23/32	6-15/16	7-23/32	6-7/8	7-25/32
76	7-3/8	7-25/32	7- 5/16	7-25/32	7- 5/16	7-27/32	7- 3/16	7-53/64	7- 3/16	7-27/32	7-1/16	7-27/32	7	7-29/32
77	7-1/2	7-29/32	7- 7/16	7-29/32	7- 7/16	7-31/32	7- 5/16	7-61/64	7- 5/16	7-31/32	7-3/16	7-31/32	7-1/8	8- 1/32
80	7-5/8	8- 1/32	7- 9/16	8- 1/32	7- 9/16	8- 3/32	7- 7/16	8- 5/64	7- 7/16	8- 3/32	7-5/16	8- 3/32	7-1/4	8- 5/32
81					7-11/16	8- 7/32					7-7/16	8- 7/32		
82											7-9/16	8-11/32		
83											7-11/16	8-15/32		
84											7-13/16	8-19/32		
85											7-15/16	8-23/32		
86											8-1/16	8-27/32		
87											8-3/16	8-31/32		

PREPARING ACTIVITY NAVY - AS

CUSTODIANS ARMY - AV NAVY - AS

AIR FORCE - 99 DLA - IS

REVIEW USER

PROJECT NUMBER 5306-1415

MILITARY SPECIFICATION SHEET

TITLE

BOLT - MACHINE, AIRCRAFT

SPECIFICATION SHEET NUMBER

AN3 THRU AN20 14 JAN 91 (12)

SUPERSEDING

AN3 THRU AN20 26 FEB 1990

AMSC - N/A FSC: 5306

DISTRIBUTION STATEMENT A Approved for public release, distribution is unlimited

DD FORM 672 MAY 1988 PREVIOUS EDITIONS OF THIS FORM ARE OBSOLETE

THE REQUIREMENTS FOR ACQUIRING THE PRODUCT(S) DESCRIBED HEREIN SHALL CONSIST OF THIS SPECIFICATION SHEET AND THE ISSUE OF THE FOLLOWING SPECIFICATION LISTED IN THAT ISSUE OF THE DODISS SPECIFIED IN THE SOLICITATION MIL - B - 6812

THIS SPECIFICATION IS APPROVED FOR USE BY ALL DEPARTMENTS AND AGENCIES OF THE DEPARTMENT OF DEFENSE

Source: https://assist.dla.mil -- Downloaded: 202640-26T14:14Z
Check the source to verify that this is the current version before use.

Form approved
OMB No. 0704-0188

THE REQUIREMENTS FOR ACQUIRING THE PRODUCT(S) DESCRIBED HEREIN SHALL CONSIST OF THIS SPECIFICATION SHEET AND THE ISSUE OF THE FOLLOWING SPECIFICATION LISTED IN THAT ISSUE OF THE DODISS SPECIFIED IN THE SOLICITATION MIL-B-6812

DASH NO	AN10 GRIP -1/64	AN10 LENGTH +1/32 -1/64	AN12 GRIP 1/64	AN12 LENGTH +1/32 -1/64	AN14 GRIP ±1/64	AN14 LENGTH +1/32 -1/64	AN16 GRIP -1/64	AN16 LENGTH +1/32 -1/64	AN17 GRIP -1/64	AN17 LENGTH +1/32 -1/64	AN18 GRIP ±1/64	AN18 LENGTH +1/32 -1/64	AN20 GRIP ±1/64	AN20 LENGTH +1/32 -1/64
7	1/16	1- 1/64												
10	3/16	1- 9/64	1/16	1- 5/32										
11	5/16	1-17/64	3/16	1- 9/32	1/16	1- 5/16								
12	7/16	1-25/64	5/16	1-13/32	3/16	1- 7/16	1/8	1-1/2	1/8	1-1/2				
13	9/16	1-33/64	7/16	1-17/32	5/16	1- 9/16	1/4	1-5/8	1/4	1-5/8	1/16	1- 9/16		
14	11/16	1-41/64	9/16	1-21/32	7/16	1-11/16	3/8	1-3/4	3/8	1-3/4	3/16	1-11/16		
15	13/16	1-49/64	11/16	1-25/32	9/16	1-13/16	1/2	1-7/8	1/2	1-7/8	5/16	1-13/16	1/8	1-13/16
16	15/16	1-57/64	13/16	1-29/32	11/16	1-15/16	5/8	2	5/8	2	7/16	1-15/16	1/4	1-15/16
17	1- 1/16	2- 1/64	15/16	2- 1/32	13/16	2- 1/16	3/4	2-1/8	3/4	2-1/8	9/16	2- 1/16	3/8	2- 1/16
20	1- 3/16	2- 9/64	1- 1/16	2- 5/32	15/16	2- 3/16	7/8	2-1/4	7/8	2-1/4	11/16	2- 3/16	1/2	2- 3/16
21	1- 5/16	2-17/64	1- 3/16	2- 9/32	1- 1/16	2- 5/16	1	2-3/8	1	2-3/8	13/16	2- 5/16	5/8	2- 5/16
22	1- 7/16	2-25/64	1- 5/16	2-13/32	1- 3/16	2- 7/16	1-1/8	2-1/2	1-1/8	2-1/2	15/16	2- 7/16	3/4	2- 7/16
23	1- 9/16	2-33/64	1- 7/16	2-17/32	1- 5/16	2- 9/16	1-1/4	2-5/8	1-1/4	2-5/8	1- 1/16	2- 9/16	7/8	2- 9/16
24	1-11/16	2-41/64	1- 9/16	2-21/32	1- 7/16	2-11/16	1-3/8	2-3/4	1-3/8	2-3/4	1- 3/16	2-11/16	1	2-11/16
25	1-13/16	2-49/64	1-11/16	2-25/32	1- 9/16	2-13/16	1-1/2	2-7/8	1-1/2	2-7/8	1- 5/16	2-13/16	1-1/8	2-13/16
26	1-15/16	2-57/64	1-13/16	2-29/32	1-11/16	2-15/16	1-5/8	3	1-5/8	3	1- 7/16	2-15/16	1-1/4	2-15/16
27	2- 1/16	3- 1/64	1-15/16	3- 1/32	1-13/16	3- 1/16	1-3/4	3-1/8	1-3/4	3-1/8	1- 9/16	3- 1/16	1-3/8	3- 1/16
30	2- 3/16	3- 9/64	2- 1/16	3- 5/32	1-15/16	3- 3/16	1-7/8	3-1/4	1-7/8	3-1/4	1-11/16	3- 3/16	1-1/2	3- 3/16
31	2- 5/16	3-17/64	2- 3/16	3- 9/32	2- 1/16	3- 5/16	2	3-3/8	2	3-3/8	1-13/16	3- 5/16	1-5/8	3- 5/16
32	2- 7/16	3-25/64	2- 5/16	3-13/32	2- 3/16	3- 7/16	2-1/8	3-1/2	2-1/8	3-1/2	1-15/16	3- 7/16	1-3/4	3- 7/16
33	2- 9/16	3-33/64	2- 7/16	3-17/32	2- 5/16	3- 9/16	2-1/4	3-5/8	2-1/4	3-5/8	2- 1/16	3- 9/16	1-7/8	3- 9/16
34	2-11/16	3-41/64	2- 9/16	3-21/32	2- 7/16	3-11/16	2-3/8	3-3/4	2-3/8	3-3/4	2- 3/16	3-11/16	2	3-11/16
35	2-13/16	3-49/64	2-11/16	3-25/32	2- 9/16	3-13/16	2-1/2	3-7/8	2-1/2	3-7/8	2- 5/16	3-13/16	2-1/8	3-13/16
36	2-15/16	3-57/64	2-13/16	3-29/32	2-11/16	3-15/16	2-5/8	4	2-5/8	4	2- 7/16	3-15/16	2-1/4	3-15/16
37	3- 1/16	4- 1/64	2-15/16	4- 1/32	2-13/16	4- 1/16	2-3/4	4-1/8	2-3/4	4-1/8	2- 9/16	4- 1/16	2-3/8	4- 1/16
40	3- 3/16	4- 9/64	3- 1/16	4- 5/32	2-15/16	4- 3/16	2-7/8	4-1/4	2-7/8	4-1/4	2-11/16	4- 3/16	2-1/2	4- 3/16
41	3- 5/16	4-17/64	3- 3/16	4- 9/32	3- 1/16	4- 5/16	3	4-3/8	3	4-3/8	2-13/16	4- 5/16	2-5/8	4- 5/16
42	3- 7/16	4-25/64	3- 5/16	4-13/32	3- 3/16	4- 7/16	3-1/8	4-1/2	3-1/8	4-1/2	2-15/16	4- 7/16	2-3/4	4- 7/16
43	3- 9/16	4-33/64	3- 7/16	4-17/32	3- 5/16	4- 9/16	3-1/4	4-5/8	3-1/4	4-5/8	3- 1/16	4- 9/16	2-7/8	4- 9/16
44	3-11/16	4-41/64	3- 9/16	4-21/32	3- 7/16	4-11/16	3-3/8	4-3/4	3-3/8	4-3/4	3- 3/16	4-11/16	3	4-11/16
45	3-13/16	4-49/64	3-11/16	4-25/32	3- 9/16	4-13/16	3-1/2	4-7/8	3-1/2	4-7/8	3- 5/16	4-13/16	3-1/8	4-13/16
46	3-15/16	4-57/64	3-13/16	4-29/32	3-11/16	4-15/16	3-5/8	5	3-5/8	5	3- 7/16	4-15/16	3-1/4	4-15/16
47	4- 1/16	5- 1/64	3-15/16	5- 1/32	3-13/16	5- 1/16	3-3/4	5-1/8	3-3/4	5-1/8	3- 9/16	5- 1/16	3-3/8	5- 1/16
50	4- 3/16	5- 9/64	4- 1/16	5- 5/32	3-15/16	5- 3/16	3-7/8	5-1/4	3-7/8	5-1/4	3-11/16	5- 3/16	3-1/2	5- 3/16
51	4- 5/16	5-17/64	4- 3/16	5- 9/32	4- 1/16	5- 5/16	4	5-3/8	4	5-3/8	3-13/16	5- 5/16	3-5/8	5- 5/16
52	4- 7/16	5-25/64	4- 5/16	5-13/32	4- 3/16	5- 7/16	4-1/8	5-1/2	4-1/8	5-1/2	3-15/16	5- 7/16	3-3/4	5- 7/16
53	4- 9/16	5-33/64	4- 7/16	5-17/32	4- 5/16	5- 9/16	4-1/4	5-5/8	4-1/4	5-5/8	4- 1/16	5- 9/16	3-7/8	5- 9/16
54	4-11/16	5-41/64	4- 9/16	5-21/32	4- 7/16	5-11/16	4-3/8	5-3/4	4-3/8	5-3/4	4- 3/16	5-11/16	4	5-11/16
55	4-13/16	5-49/64	4-11/16	5-25/32	4- 9/16	5-13/16	4-1/2	5-7/8	4-1/2	5-7/8	4- 5/16	5-13/16	4-1/8	5-13/16
56	4-15/16	5-57/64	4-13/16	5-29/32	4-11/16	5-15/16	4-5/8	6	4-5/8	6	4- 7/16	5-15/16	4-1/4	5-15/16
57	5- 1/16	6- 1/64	4-15/16	6- 1/32	4-13/16	6- 1/16	4-3/4	6-1/8	4-3/4	6-1/8	4- 9/16	6- 1/16	4-3/8	6- 1/16
60	5- 3/16	6- 9/64	5- 1/16	6- 5/32	4-15/16	6- 3/16	4-7/8	6-1/4	4-7/8	6-1/4	4-11/16	6- 3/16	4-1/2	6- 3/16
61	5- 5/16	6-17/64	5- 3/16	6- 9/32	5- 1/16	6- 5/16	5	6-3/8	5	6-3/8	4-13/16	6- 5/16	4-5/8	6- 5/16
62	5- 7/16	6-25/64	5- 5/16	6-13/32	5- 3/16	6- 7/16	5-1/8	6-1/2	5-1/8	6-1/2	4-15/16	6- 7/16	4-3/4	6- 7/16
63	5- 9/16	6-33/64	5- 7/16	6-17/32	5- 5/16	6- 9/16	5-1/4	6-5/8	5-1/4	6-5/8	5- 1/16	6- 9/16	4-7/8	6- 9/16
64	5-11/16	6-41/64	5- 9/16	6-21/32	5- 7/16	6-11/16	5-3/8	6-3/4	5-3/8	6-3/4	5- 3/16	6-11/16	5	6-11/16
65	5-13/16	6-49/64	5-11/16	6-25/32	5- 9/16	6-13/16	5-1/2	6-7/8	5-1/2	6-7/8	5- 5/16	6-13/16	5-1/8	6-13/16
66	5-15/16	6-57/64	5-13/16	6-29/32	5-11/16	6-15/16	5-5/8	7	5-5/8	7	5- 7/16	6-15/16	5-1/4	6-15/16
67	6- 1/16	7- 1/64	5-15/16	7- 1/32	5-13/16	7- 1/16	5-3/4	7-1/8	5-3/4	7-1/8	5- 9/16	7- 1/16	5-3/8	7- 1/16
70	6- 3/16	7- 9/64	6- 1/16	7- 5/32	5-15/16	7- 3/16	5-7/8	7-1/4	5-7/8	7-1/4	5-11/16	7- 3/16	5-1/2	7- 3/16
71	6- 5/16	7-17/64	6- 3/16	7- 9/32	6- 1/16	7- 5/16	6	7-3/8	6	7-3/8	5-13/16	7- 5/16	5-5/8	7- 5/16
72	6- 7/16	7-25/64	6- 5/16	7-13/32	6- 3/16	7- 7/16	6-1/8	7-1/2	6-1/8	7-1/2	5-15/16	7- 7/16	5-3/4	7- 7/16
73	6- 9/16	7-33/64	6- 7/16	7-17/32	6- 5/16	7- 9/16	6-1/4	7-5/8	6-1/4	7-5/8	6- 1/16	7- 9/16	5-7/8	7- 9/16
74	6-11/16	7-41/64	6- 9/16	7-21/32	6- 7/16	7-11/16	6-3/8	7-3/4	6-3/8	7-3/4	6- 3/16	7-11/16	6	7-11/16
75	6-13/16	7-49/64	6-11/16	7-25/32	6- 9/16	7-13/16	6-1/2	7-7/8	6-1/2	7-7/8	6- 5/16	7-13/16	6-1/8	7-13/16
76	6-15/16	7-57/64	6-13/16	7-29/32	6-11/16	7-15/16	6-5/8	8	6-5/8	8	6- 7/16	7-15/16	6-1/4	7-15/16
77	7- 1/16	8- 1/64	6-15/16	8- 1/32	6-13/16	8- 1/16	6-3/4	8-1/8	6-3/4	8-1/8	6- 9/16	8- 1/16	6-3/8	8- 1/16
80	7- 3/16	8- 9/64	7- 1/16	8- 5/32	6-15/16	8- 3/16	6-7/8	8-1/4	6-7/8	8-1/4	6-11/16	8- 3/16	6-1/2	8- 3/16
81							7	8-3/8	7-	8-3/8	6-13/16	8- 5/16	6-5/8	8- 5/16
82							7-1/8	8-1/2	7-1/8	8-1/2				

(b) GRIP LENGTH OF BOLTS SHALL BE MEASURED FROM THE UNDERSIDE OF THE HEAD TO THE END OF THE FULL CYLINDRICAL PORTION OF THE SHANK. COMPLETE THREADS SHALL BEGIN WITHIN TWO THREAD PITCH MAXIMUM. TWO THREAD PITCH MAXIMUM MAY CONSIST OF INCOMPLETE THREAD OR EXTRUSION ANGLE.

PREPARING ACTIVITY NAVY - AS CUSTODIANS ARMY - AV NAVY - AS AIR FORCE - 99 DLA - IS REVIEW USER PROJECT NUMBER 5306-1415	MILITARY SPECIFICATION SHEET TITLE BOLT - MACHINE, AIRCRAFT	SPECIFICATION SHEET NUMBER AN3 THRU AN20 14 JAN 91 (12) SUPERSEDING AN3 THRU AN20 26 FEB 90 AMSC - N/A FSC 5306

DISTRIBUTION STATEMENT A. Approved for public release; distribution is unlimited.

THIS SPECIFICATION IS APPROVED FOR USE BY ALL DEPARTMENTS AND AGENCIES OF THE DEPARTMENT OF DEFENSE

DD FORM 672 MAY 1988 PREVIOUS EDITIONS OF THIS FORM ARE OBSOLETE

Source: https://assist.dla.mil -- Downloaded: 20260-26T14:14Z
Check the source to verify that this is the current version before use.

THE REQUIREMENTS FOR ACQUIRING THE PRODUCT(S) DESCRIBED HEREIN SHALL CONSIST OF THIS SPECIFICATION SHEET AND THE ISSUE OF THE FOLLOWING SPECIFICATION LISTED IN THAT ISSUE OF THE DODISS SPECIFIED IN THE SOLICITATION MIL-B-6812

THIS SPECIFICATION IS APPROVED FOR USE BY ALL DEPARTMENTS AND AGENCIES OF THE DEPARTMENT OF DEFENSE

Form approved
OMB No. 0704-0188

BASIC AN PART NO	THREAD T	RATED STRENGTH (POUNDS) ULTIMATE TENSILE AT ROOT DIA STEEL	ULTIMATE TENSILE AT ROOT DIA AL ALLOY	YIELD TENSILE AT ROOT DIA STEEL	YIELD TENSILE AT ROOT DIA AL ALLOY	SINGLE SHEAR AT FULL DIA STEEL	SINGLE SHEAR AT FULL DIA AL ALLOY
AN3	NO 10-32 UNF-3A	2,210	1,100	1,690	710	2,125	990
AN4	1/4 -28 UNF-3A	4,080	2,030	3,130	1,310	3,680	1,715
AN5	5/16-24 UNF-3A	6,500	3,220	4,980	2,080	5,750	2,685
AN6	3/8 -24 UNF-3A	10,100	5,020	7,740	3,240	8,280	3,870
AN7	7/16-20 UNF-3A	13,600	6,750	10,430	4,350	11,250	5,250
AN8	1/2 -20 UNF-3A	18,500	9,180	14,190	5,920	14,700	6,850
AN9	9/16-18 UNF-3A	23,600	11,700	18,100	7,550	18,700	8,700
AN10	5/8 -18 UNF-3A	30,100	14,900	23,080	9,610	23,000	10,750
AN12	3/4 -16 UNF-3A	44,000	21,800	33,730	14,100	33,150	15,500
AN14	7/8 -14 UNF-3A	60,000	29,800	46,000	19,200	45,050	21,050
~~AN16~~	~~1 -14 NF-3A~~	~~80,700~~	~~40,000~~	~~61,870~~	~~25,800~~	~~58,900~~	~~27,500~~
AN17	1 -12UNF-3A	80,700	40,000	61,870	25,800	58,900	27,500
AN18	1-1/8 -12 UNF-3A	101,800	50,500	78,050	32,600	73,750	34,500
AN20	1-1/4 -12 UNF-3A	130,200	64,400	99,820	41,500	91,050	42,500

PREPARING ACTIVITY NAVY-AS
CUSTODIANS ARMY-AV NAVY-AS
AIR FORCE-99 DLA-IS
REVIEW
USER
PROJECT NUMBER 5306-1415

MILITARY SPECIFICATION SHEET

TITLE

BOLT - MACHINE, AIRCRAFT

SPECIFICATION SHEET NUMBER
AN3 THRU AN20 14 JAN 91 (12)

SUPERSEDING
AN3 THRU AN20 26 FEB 90

AMSC- N/A FSC: 5306

DISTRIBUTION STATEMENT A Approved for public release distribution is unlimited

DD FORM 672 MAY 1988 PREVIOUS EDITIONS OF THIS FORM ARE OBSOLETE

Source: https://assist.dla.mil -- Downloaded: 202610-26T14:14Z
Check the source to verify that this is the current version before use.