
DISTRIBUTION STATEMENT A. Approved for public release; distribution is unlimited.

AMSC/N/A

NOTE: This drawing was approved by joint action of the Air Force and Navy Departments as the Air Force-Navy standard for this product. This drawing supersedes all previously standard drawings for the same product and shall become effective for the procurement of successful supplies, or for use in new designs, not later than 6 months after the latest date of approval shown.

NOTICE: When Government drawings, specifications, or other data are used for any purpose other than in connection with a definitely related Government procurement operation, the United States Government thereby incurs no responsibility, nor any obligation whatsoever; and the fact that the Government may have formulated, furnished, or in any way supplied the said drawings, specifications, or other data is not to be regarded by implication or otherwise as in any manner licensing the holder or any other person or corporation, or conveying any rights or permission to manufacture, use, or sell any patented invention that may in any way be related thereto.

FSC 6610

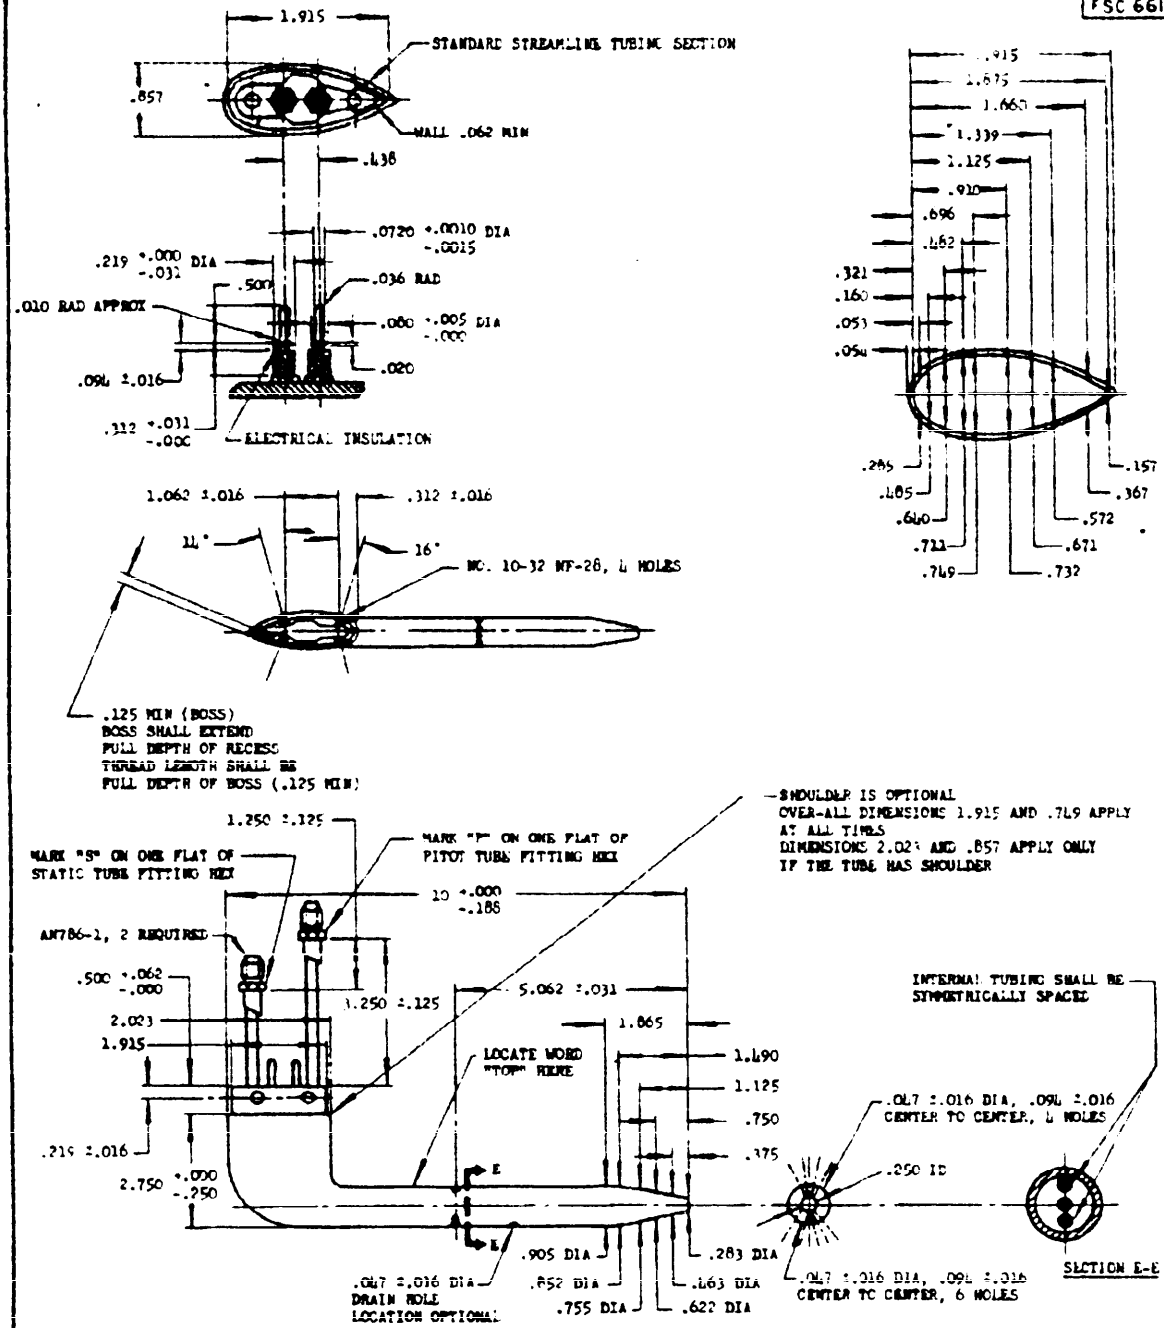

AN PART NO.	RATED VOLTAGE
(a) ~~AN5811-1~~	~~28-VOLT DIRECT CURRENT~~
AN5811-2	28-VOLT DIRECT CURRENT
AN5811-3	115-VOLT, 400-CYCLE, SINGLE-PHASE ALTERNATING CURRENT

(a) AN PART NUMBER AN5811-1 CANCELED AFTER 7 MARCH 1951.
FOR DEFINITION AND APPLICATION OF DRAWING STATUS NOTES, SEE AMA BULLETIN NO. 337.
ROUNDED TRAILING EDGE OF STREAMLINE TUBING SECTION LIMITED TO .0625 RADIUS.
DIMENSIONS IN INCHES. UNLESS OTHERWISE SPECIFIED, TOLERANCES: DECIMALS ±.010, ANGLES ±1/2°.

(9) Cancelled --- No Superseding Document.

PROCUREMENT SPECIFICATION	AIR FORCE-NAVY AERONAUTICAL STANDARD	AN5814
MIL-T-5420	TUBE, PITOT STATIC, "L" SHAPED, ELECTRICALLY HEATED	

6610-0243

APPROVED 12 Aug 43 REVISED (1) 14 Feb 47 (2) 7 Mar 51 (3) 27 Feb 52 (4) 21 Oct 52 (5) 17 Sep 53 (6) 10 Jun 54 (7) 1 Mar 55 (8) 30 Nov 55 (9) 25 Apr 11 1988

NOTE TO PRINTER: REDUCE BORDER FROM ORIGINAL 11-3/8x16-1/4 TO 6-27/32x9-3/4.
PRINT LEFT BORDER-LINE ONE INCH FROM LEFT EDGE OF 8x16-1/2 SHEET.
PRINT BOTTOM BORDER LINE 0.5 INCH FROM BOTTOM EDGE OF 8x16-1/2 SHEET.
SIGNATURE FORM NOT TO BE PRINTED ON STANDARD BOOK SHEET.

DRAWN BY
TYPED BY L.M.S. DATE 1 NOV 88
CHECKED BY

Downloaded from http://www.everyspec.com on 2026-10-26T14:21Z
Check the source to verify that this is the current version before use.