MILITARY STANDARD

MIL STD 1325-137


LOADING

(NAVY)

FIN ASSEMBLY, BOMB FOR 2000 LB G P BOMB MK 84
IN CRATE MX 13 MOD 1
FLEET ISSUE UNIT LOAD

UNIT LOAD DATA

UNIT LOAD DRAWING	MX-54 240
WEIGHT	710 LBS
DIMENSIONS	51 1/2 L x 40 W x 44 3/4 H
CUBE	53.3 CU FT
DOT HAZARD CLASSIFICATION	1.1

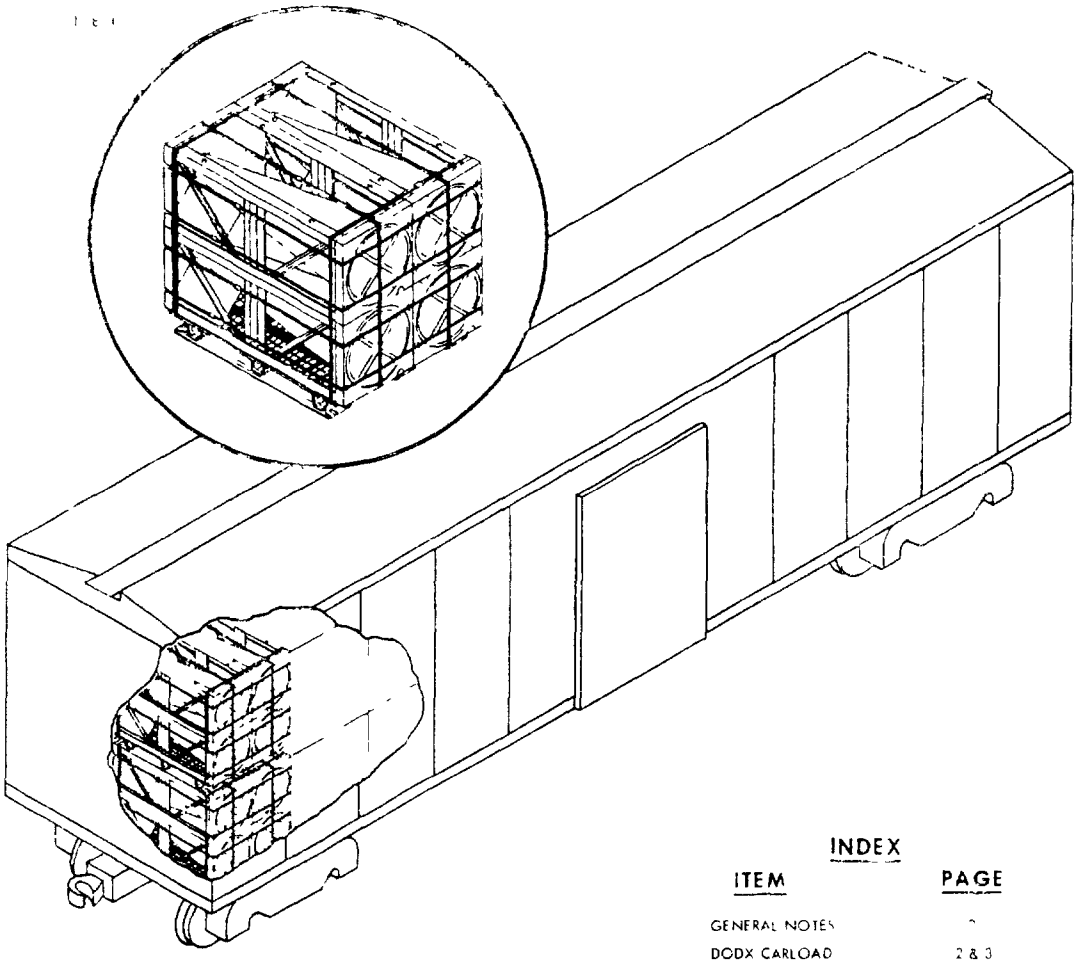

INDEX

ITEM	PAGE
GENERAL NOTES	2
DODX CARLOAD	2 & 3
40 -6 CARLOAD COM	4 & 5
50 -6 CARLOAD COML	6 & 7

NOTES

1. UNLESS OTHERWISE SPECIFIED DIMENSIONS ARE IN INCHES
2. FOR CROSS REFERENCE TO ASSOCIATED PALLETIZING, TRUCKLOADING AND CONTAINERLOADING MILITARY STANDARDS REFER TO INDEX TO STANDARDS MIL-HDBK-236 (NAVY)

AUTHORIZED AND RELEASED FOR GENERAL USE

M S Gray NYPHI 4/19/83
SIGNATURE TECHNICAL DIRECTIVE AGENT (NDA) DATE

J. E. Kelly 4/20/83
SIGNATURE (AIR) / SYSCOM DIRECTION DATE

APPROVED BY BUREAU OF EXPLOSIVES

NOT APPLICABLE

MILITARY ASSISTANT

SIGNATURE DATE

ORIGINATOR Charles McBride 4/19/83
SIGNATURE

WEAPONS HANDLING LABORATORY
NAD EARLE, NEW JERSEY

Source: https://assist.dla.mil -- Downloaded: 2026-10-24T00:02Z
Check the source to verify that this is the current version before use.

GENERAL NOTES

1 FOR GENERAL INFORMATION CONCERNING ORDERING, INSPECTING AND PREPARING CARS AND FOR DUNNAGING MATERIALS, DESIGN, AND INSTALLATION OF DUNNAGE SEE THE GENERAL DOCUMENT MIL-STD-1325 (NAVY) "RAILCAR LOADING OF HAZARDOUS MATERIALS."

2 WHEN PLANNING SHIPMENTS ORDER THE MINIMUM NUMBER OF CARS OF THE CAPACITY REQUIRED FOR THE SHIPMENT. UTILITY LOADER CARS SHALL BE SERIES DODX 28000

3 LOADING PLANS SHOWN ARE FOR DODX UTILITY LOADER CAR WITH 50 FT 6 INCHES INSIDE LENGTH, 10'5 4 INCHES INSIDE WIDTH BETWEEN RAILS (111 INCHES INSIDE WIDTH BETWEEN SIDE WALLS. COMMERCIAL BOXCARS WITH 40 FT 6 INCHES INSIDE LENGTH, 110 INCHES INSIDE WIDTH, AND COMMERCIAL BOXCARS WITH 50 FT 6 INCHES INSIDE LENGTH, 110 INCHES INSIDE WIDTH

4 THE "LOAD LIMIT" OF A CAR MUST NOT BE EXCEEDED NOR SHOULD THE RAILCAR BE LOADED SO THAT MORE THAN ONE-HALF OF THE "LOAD LIMIT" IS CARRIED BY ONE SET OF TRUCKS

5 IF END WALLS OF CARS ARE NOT SQUARE THEY MUST BE SQUARED OFF BEFORE STARTING TO LOAD CAR

6 THE LOAD CONSISTS OF BOMB FIN ASSEMBLIES FOR 2000 LB G.P. MK 84 BOMBS IN MK 1 MOD 1 CRATES PALLETIZED IN ACCORDANCE WITH WR-51/240

7 THE UNIT LOADS ARE HANDLED AND LOADED WITH A SUITABLE FORK LIFT TRUCK

8 UNLESS OTHERWISE SPECIFIED NAILING SHALL BE IN ACCORDANCE WITH MIL-STD-1325 (NAVY)

9 ALL STRAP JOINTS SHALL BE CRIMP-TYPE JOINTS MADE WITH A CRIMPING TOOL THAT DOES NOT CUT THE SEAL OR STRAP, RATHER THAN A TOOL THAT MAKES A NOTCH-TYPE JOINT. THE STRAPPING MUST BE IN ACCORDANCE WITH NAVSUP NOTICE 4642 DATED 2, APRIL 1971

10 APPLICABLE MATERIAL SPECIFICATIONS

DUNNAGE LUMBER - FED. SPEC. MM-L-751

NAILS - FED. SPEC. FF-N-105

STRAPPING - FED. SPEC. QQ-S-781, TYPE I, HEAVY DUTY, CLASS A, DRY (UNLUBRICATED)

SEALS - FED. SPEC. QQ-S-781, STYLE III, HEAVY DUTY

11 AFTER BLOCKING AND BRACING HAS BEEN INSPECTED ATTACH SHIPPING DOCUMENTS INSIDE THE CAR IN AN ACCESSIBLE AREA, CLOSE AND SEAL BOXCAR DOORS


50 FT 6 IN. BOXCAR, DODX

1 THE CARLOAD CONSISTS OF 56 UNIT LOADS WHICH MUST BE LOADED AND DUNNAGED IN ACCORDANCE WITH THE PROCEDURAL DRAWING

2 A DETAILED DESCRIPTION AND OPERATING INSTRUCTIONS FOR THE UTILITY LOADER ARE CONTAINED IN OP 1/50

3 TO PREVENT UNUSED "DF" EQUIPMENT FROM BECOMING DISLODGED DURING TRANSIT OF DODX CARS SECURE IT AT ANY LOCATION IN THE BOXCAR WHICH WILL NOT INTERFERE WITH UNLOADING


4 WHEN LESS THAN CARLOAD (LCL) QUANTITIES ARE REQUIRED TO BE SHIPPED IN DODX BOXCARS THE SAME PROCEDURES AND METHODS OF BLOCKING ARE APPLICABLE. ANY BAYS OR PORTION THEREOF MAY BE USED PROVIDING THE "WEIGHT DISTRIBUTION REQUIREMENTS" OF THE AAR ARE COMPLIED WITH. SEE MIL-STD-1325 (NAVY). EACH CROSSMEMBER WILL BE USED IN SUCH A MANNER THAT IT WILL RETAIN NOT MORE THAN 2200 LBS OF THE LADING

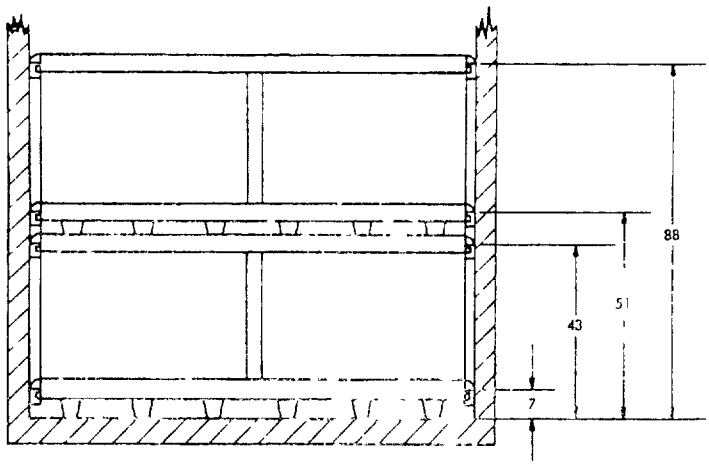

SECTION A-A

SHOWING LOCATION OF WALL MEMBERS AND DOORWAY MEMBERS USED FOR CROSSMEMBERS

Source: https://assist.dla.mil -- Downloaded: 2026-10-24T00:02Z
Check the source to verify that this is the current version before use.

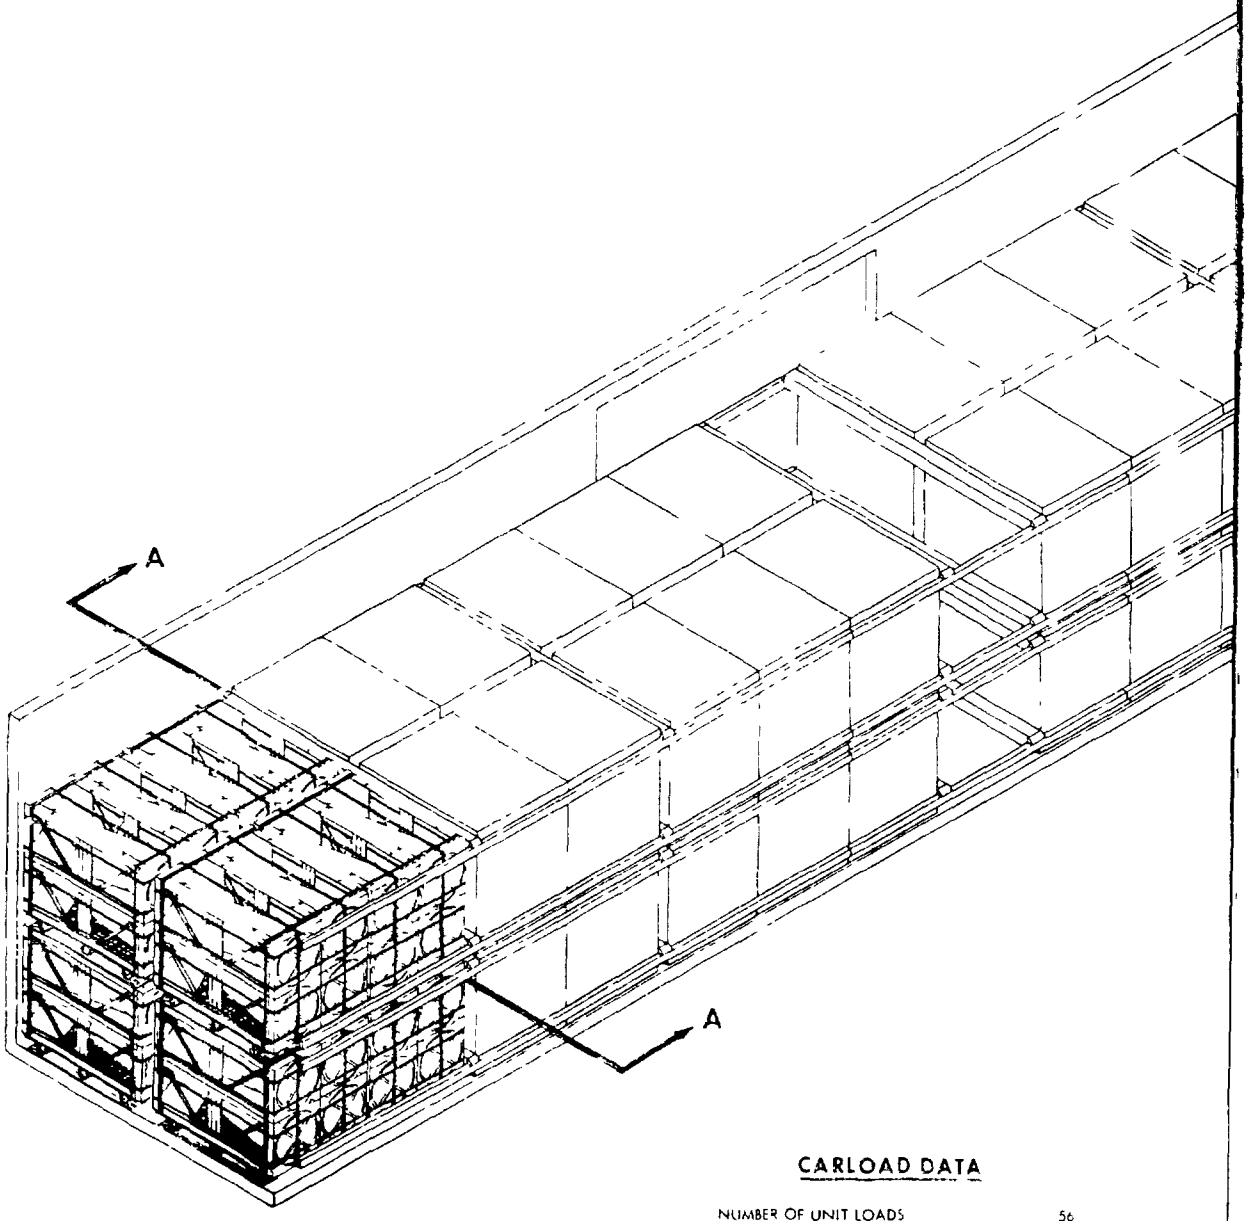


CARLOAD DATA

NUMBER OF UNIT LOADS	56
NUMBER OF CROSSMEMBERS REQ D	24
CARLOAD WEIGHT	3, 760 LBS

Source: https://assist.dla.mil -- Downloaded: 2026-10-24T00:02Z
Check the source to verify that this is the current version before use.

40 FT 3 IN BOXCAR, COMMERCIAL

1. THE CAR LOAD CONSISTS OF 44 UNIT LOADS WHICH MUST BE LOADED AND DUNNAGED IN ACCORDANCE WITH THIS PROCEDURAL DRAWING.
2. WHEN LESS THAN THE FULL LOAD QUANTITIES ARE REQUIRED TO BE SHIPPED IN COMMERCIAL BOXCARS AND A PARTIAL LAYER RESULTS, THE PARTIAL LAYER LOADING SHALL BE BRACED BY MEANS OF END BRACING AND OR PARTIAL LAYER BRACING CONSTRUCTED IN ACCORDANCE WITH MIL-STD-2100 SELECT THE TYPE OF BRACE TO COMPLY WITH THE WEIGHT OF THE UNITS TO BE RESTRAINED. THE CENTER GATE HEIGHT SHOULD BE ADJUSTED AS REQUIRED. THE WEIGHT DISTRIBUTION REQUIREMENTS OF THE AAR MUST BE COMPLIED WITH. SEE MIL-STD-1325 (NAVY).
3. THE LOADS AS SHOWN ARE BASED ON CARS WHICH HAVE 6 FT WIDE DOORWAY OPENINGS AND ARE EQUIPPED WITH CONVENTIONAL SLIDING TYPE DOORS. THE DEPICTED PROCEDURES AND METHODS OF BLOCKING ARE APPLICABLE TO BOXCARS EQUIPPED WITH CONVENTIONAL SLIDING TYPE DOORS OTHER THAN 6 FT WIDE.

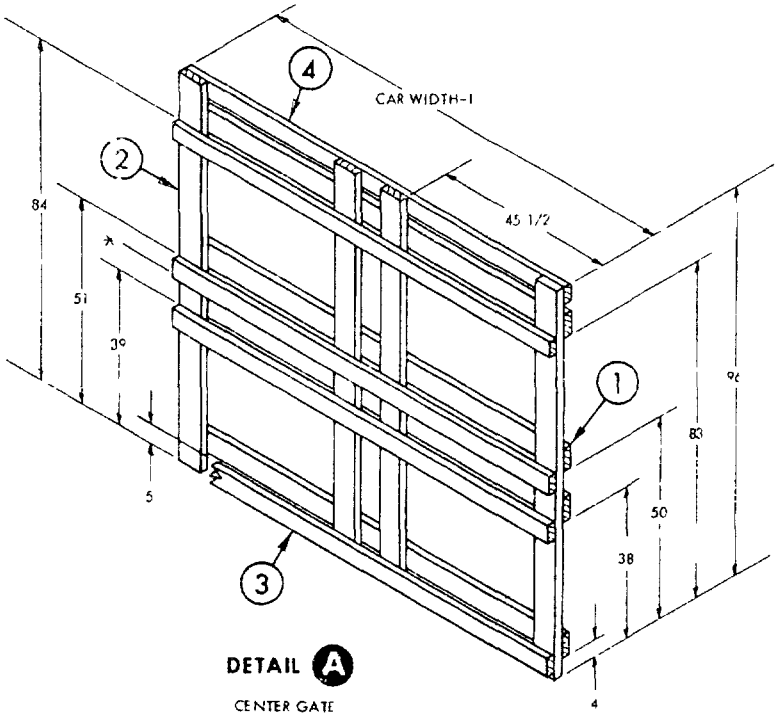

DETAIL A

CENTER GATE
2 REQUIRED


* POSITION AFTER STRUTS HAVE BEEN INSTALLED ON LOWER STRUT CLEAT (REQUIRED ONE GATE ONLY)

** 2 x 6 STRUTS DOUBLED AND LAMINATED 4 x 4 EQUIVALENTS MAY BE SUBSTITUTED IN LIEU OF 4 x 4 S


PIECE NO	DESCRIPTION	SIZE	NO PCS REQD	NAIL TO	NAILS NUMBER	NAILS SIZE
9	HORIZONTAL DOORWAY MEMBER	2 x 4 x DOOR WIDTH	8	8	2 PER JOINT	10d
8	VERTICAL DOORWAY MEMBER	2 x 3 x 96	4	DOOR POST	2 PER FOOT	20d
7	HOLD DOWN CLEAT	2 x 6 x 24	4	6	5	10d
6	GATE HOLD DOWN	2 x 6 x 10 FT	2	CAR WALL	5 EACH END	10d
5	STRUT	4 x 4 x WEDGE FIT **	16	2	2 PER JOINT	16d
4	TOP HORIZONTAL	2 x 4 x CAR WIDTH-1	2	2	3 PER JOINT	10d
3	CENTER GATE STRUT CLEAT	2 x 4 x CAR WIDTH-1	8	2	3 PER JOINT	10d
2	CENTER GATE VERTICAL	2 x 6 x 96	8	SEE 1	-	-
1	CENTER GATE HORIZONTAL	2 x 6 x CAR WIDTH-1	8	2	3 PER JOINT	10d

LIST OF MATERIALS AND NAILING DATA

Source: https://assist.dla.mil -- Downloaded: 2026-10-24T00:02Z
Check the source to verify that this is the current version before use.

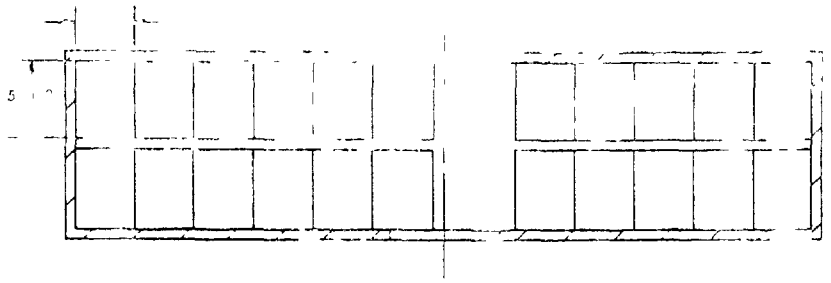


LOADING PLAN

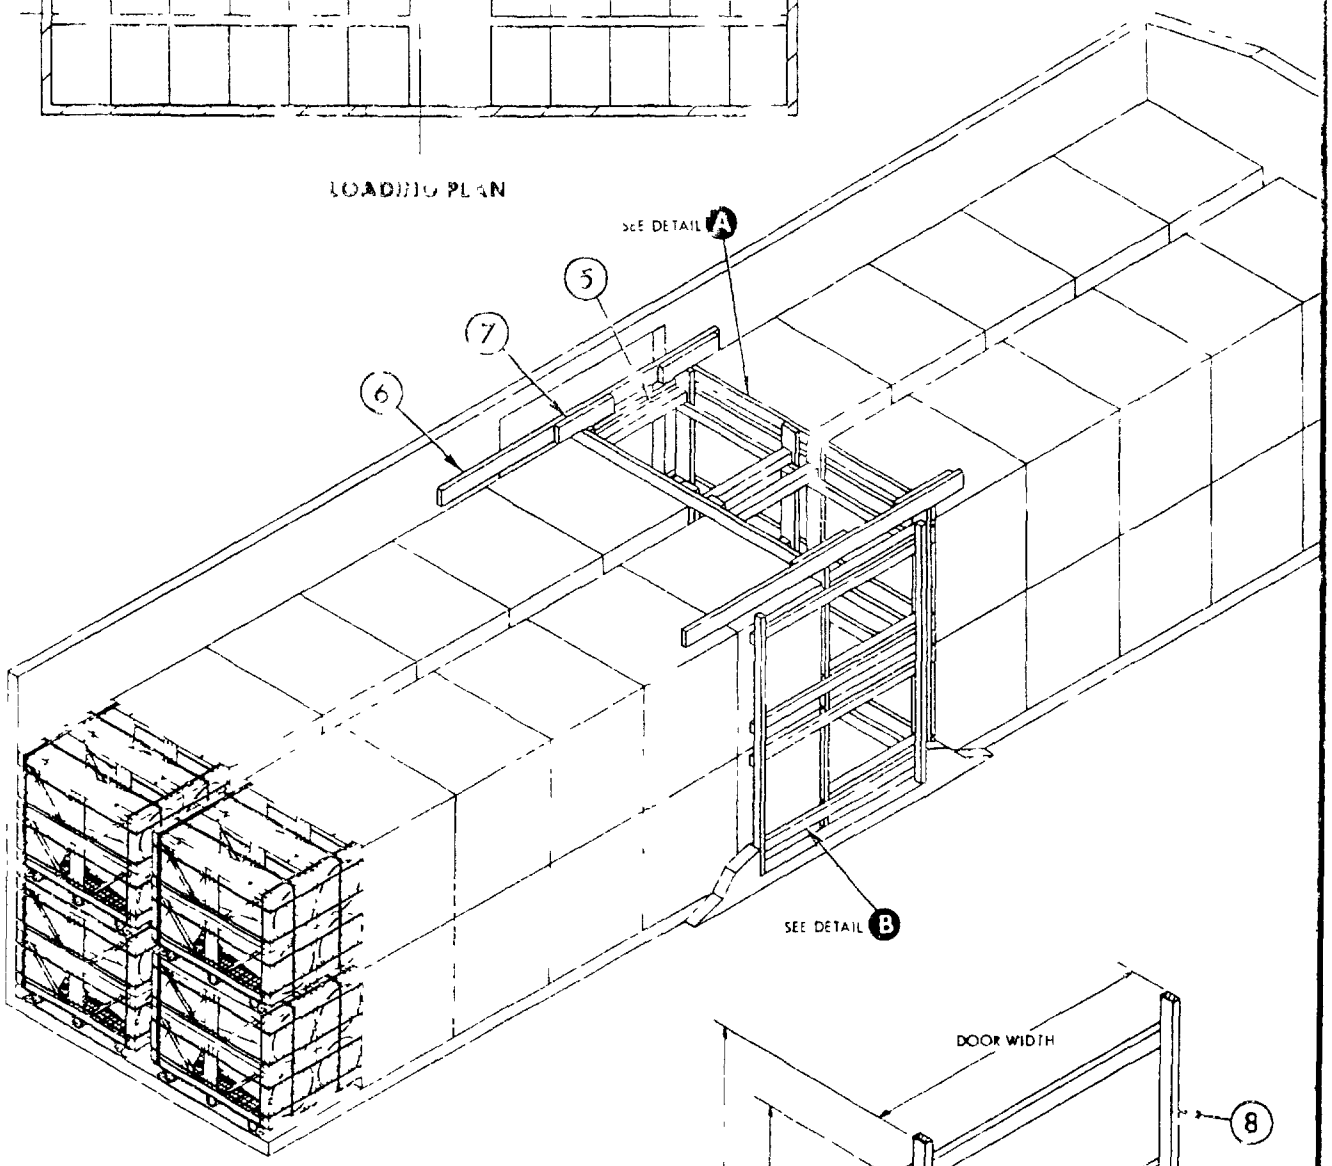

CARLOAD DATA

NUMBER OF UNIT LOADS	44
LOAD WEIGHT	3 240 LBS
DUNNAGE WEIGHT	940 LBS
CARLOAD WEIGHT	32 180 LBS

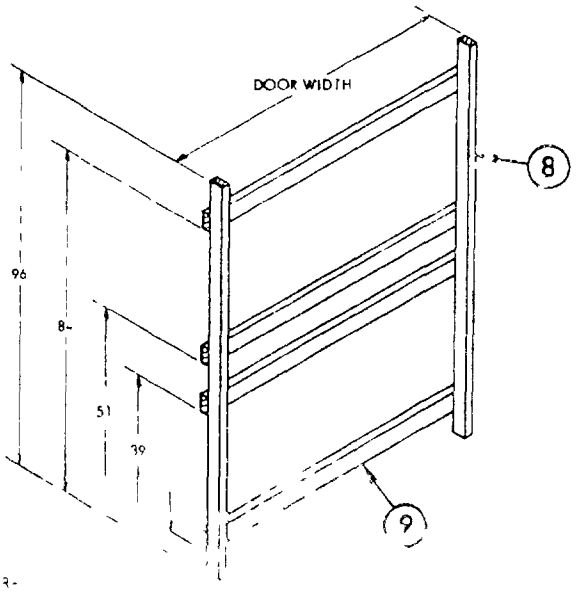

DETAIL B


2 REQUIRED

Source: https://assist.dla.mil -- Downloaded: 2026-10-24T00:02Z
Check the source to verify that this is the current version before use.

MIL-STD-1367 (NAVY)

50 FT 6 IN. BOXCAR, COMMERCIAL

1. THE CARLOAD CONSISTS OF 56 UNIT LOADS WHICH MUST BE LOADED AND DUNNAGED IN ACCORDANCE WITH THIS PROCEDURAL DRAWING
2. WHEN LESS THAN CARLOAD (LCL) QUANTITIES ARE REQUIRED TO BE SHIPPED IN COMMERCIAL BOXCARS AND A PARTIAL LAYER RESULTS THE PARTIAL LAYER OF LADING SHALL BE BRACED BY MEANS OF END BRACING AND OR PARTIAL LAYER BRACING CONSTRUCTED IN ACCORDANCE WITH WR 52 100 SELECT THE TYPE OF BRACE TO COMPLY WITH THE WEIGHT OF THE UNITS TO BE RETAINED THE CENTER GATE HEIGHT SHOULD BE ADJUSTED AS REQUIRED THE WEIGHT DISTRIBUTION REQUIREMENTS OF THE AAR MUST BE COMPLIED WITH SEE MIL-STD-1325 (NAVY)
3. THE LOADS AS SHOWN ARE BASED ON CARS WHICH HAVE 10 FT WIDE DOORWAY OPENING AND ARE EQUIPPED WITH CONVENTIONAL SLIDING TYPE DOORS THE DEPICTED PROCEDURES AND METHODS OF BLOCKING ARE APPLICABLE TO BOXCARS EQUIPPED WITH CONVENTIONAL SLIDING TYPE DOORS OTHER THAN 10 FT WIDE PROVIDING THE LENGTH OF PIECE 6 IS ADJUSTED AS REQUIRED TO SUIT THE PARTICULAR DOORWAY OPENING
4. THE DEPICTED PROCEDURES AND METHODS OF BLOCKING ARE ALSO APPLICABLE TO BOXCARS EQUIPPED WITH PLUG TYPE DOORS PROVIDING THE LENGTH OF PIECE 6 IS ADJUSTED AS REQUIRED TO SUIT THE PARTICULAR DOORWAY OPENING DUNNAGE MATERIAL MUST NOT BE NAILED TO ANY PLUG DOOR, WHETHER MAIN OR AUXILIARY EXCEPT WHEN THE CAR HAS A COMBINATION OF A CONVENTIONAL SLIDING TYPE DOOR AND A PLUG TYPE DOOR AND AN ADEQUATE NAILING STRIP IS PROVIDED ON THE PLUG TYPE DOOR IF LUMBER OF SUFFICIENT LENGTH TO SPAN PLUG DOORS IS NOT AVAILABLE RANDOM LENGTH MATERIAL DOUBLED AND SPLICED BUT WITH JOINTS OF SPLICES OFFSET MAY BE USED STACKS WITH MORE THAN HALF OF THE UNIT LOAD IN THE DOORWAY AREA MUST BE UNITIZED WITH TWO LATERALLY APPLIED 1 1/4 in STEEL STRAPS PER STACK EACH TENSIONED AND SEALED WITH TWO DOUBLE CRIMPED SEALS AND DOORWAY PROTECTION, PIECES 8 AND 9, IS NOT REQUIRED WHEN PLUG DOOR EQUIPPED BOXCARS ARE USED EXCEPT WHEN CAR HAS A COMBINATION OF PLUG DOOR AND CONVENTIONAL SLIDING DOOR THEN DOORWAY PROTECTION IS REQUIRED FOR THE CONVENTIONAL DOOR SECURELY CLOSE DOOR AND WIRE TOGETHER WITH A STRONG FLEXIBLE STEEL WIRE INSERTED THROUGH THE HOLES IN THE DOOR LATCH ASSEMBLY ONE OR MORE TIMES AND THE WIRE ENDS TWISTED TOGETHER

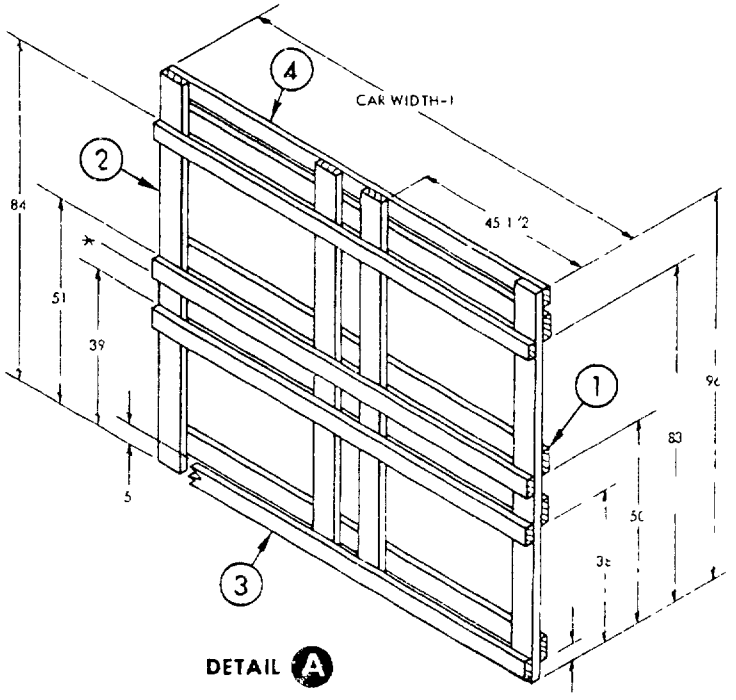

DETAIL A


CENTER GATE
2 REQUIRED

* POSITION AFTER STRUTS HAVE BEEN INSTALLED ON LOWER STRUT CLEAT (REQUIRED ONE GATE ONLY

** 2 x 6 STRUTS DOUBLED AND LAMINATED WITH 10d NAILS MAY BE SUBSTITUTED IN PLACE OF 4 x 4 S

PIECE NO	DESCRIPTION	SIZE	REQUIRED	NAILED TO	NAILING SCHEDULE	NAIL SIZE
9	HORIZONTAL DOORWAY MEMBER	2 x 4 x DOOR WIDTH	8	B	2 PER JOINT	10d
8	VERTICAL DOORWAY MEMBER	2 x 3 x 96	4	DOOR POST	2 PER FOOT	20d
7	HOLD DOWN CLEAT	2 x 6 x 24	4	6	5	10d
6	GATE HOLD DOWN	2 x 6 x 14 FT	2	CAR WALL	5 EACH END	10d
5	STRUT	4 x 4 x WEDGE FIT **	16	2	2 PER JOINT	16d
4	TOP HORIZONTAL	2 x 4 x CAR WIDTH-1	2	2	3 PER JOINT	3d
3	CENTER GATE STRUT CLEAT	2 x 4 x CAR WIDTH-1	6	4	3 PER JOINT	3d
2	CENTER GATE VERTICAL	2 x 6 x 96	8	SEE 1	-	-
1	CENTER GATE HORIZONTAL	2 x 6 x CAR WIDTH-1	6	2	3 PER JOINT	3d

Source: https://assist.dla.mil -- Downloaded: 2026-10-24T00:02Z
Check the source to verify that this is the current version before use.

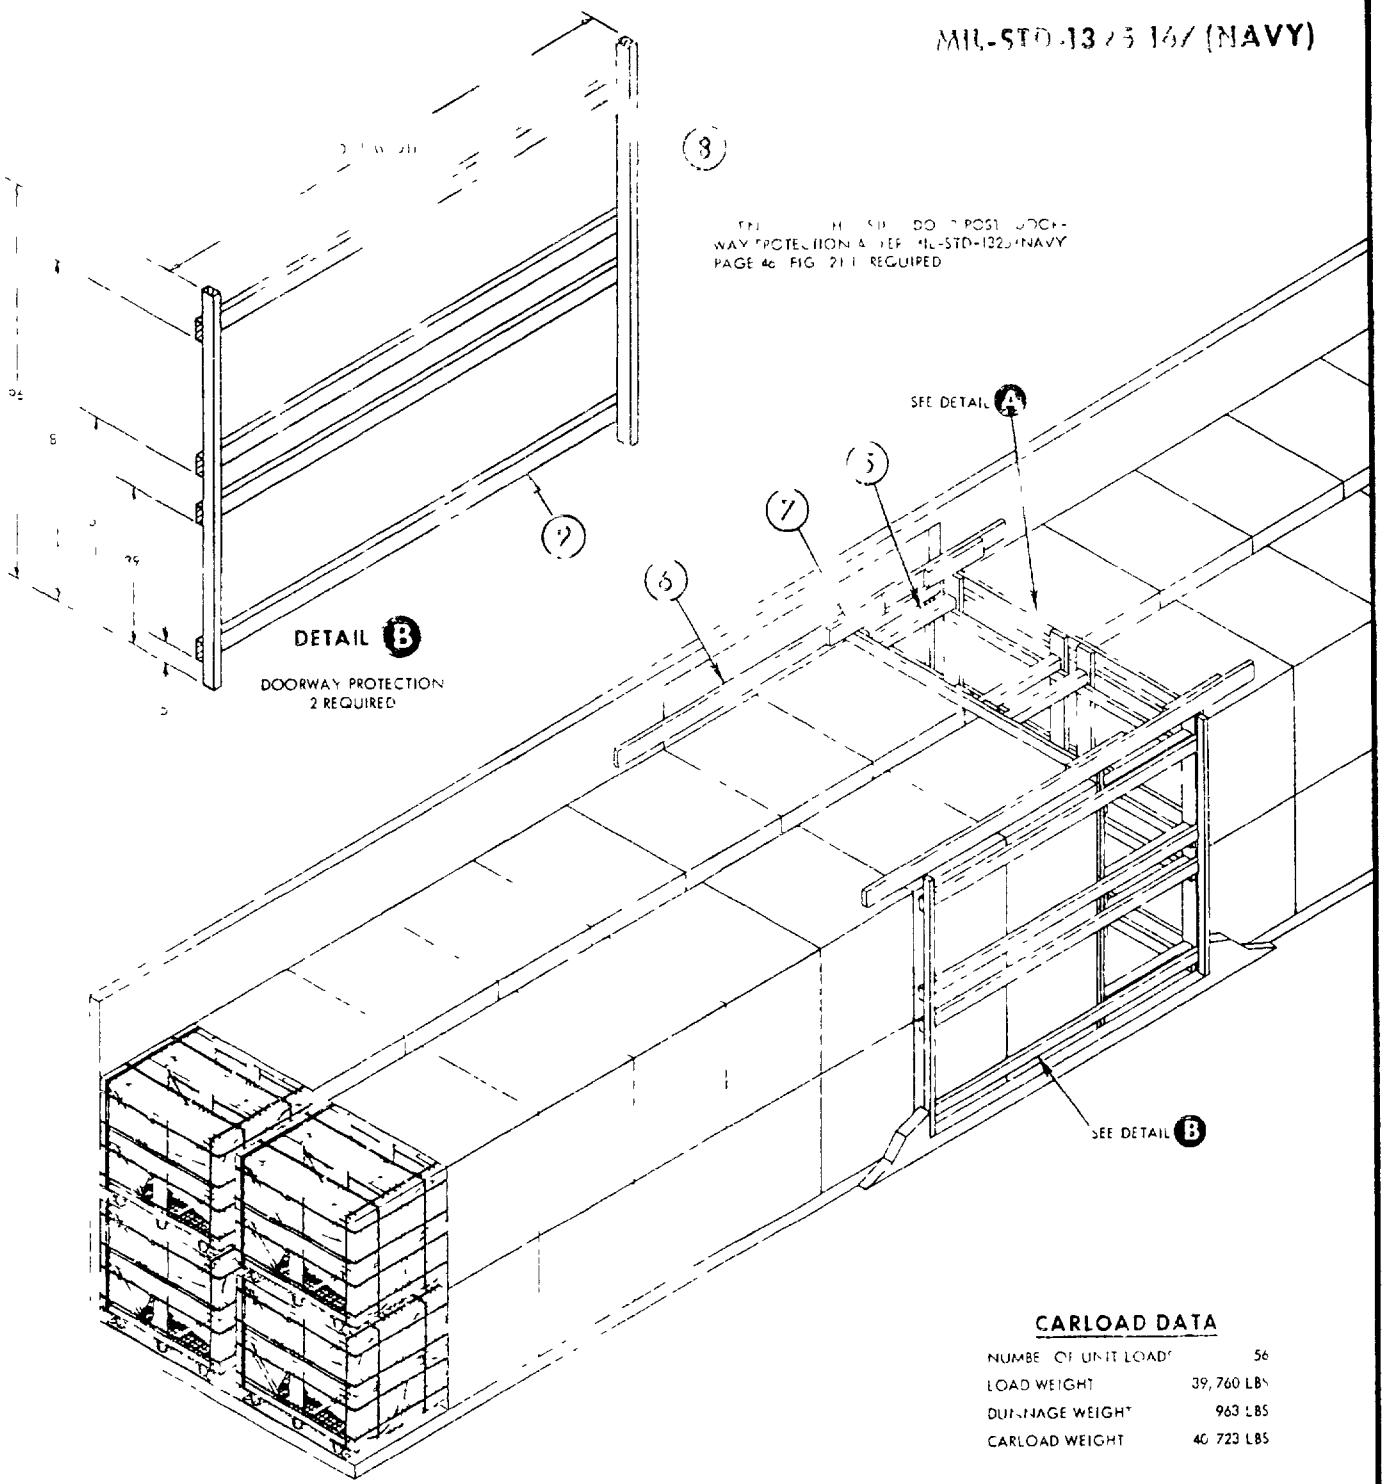


DETAIL B

DOORWAY PROTECTION
2 REQUIRED

CARLOAD DATA

NUMBER OF UNIT LOADS	56
LOAD WEIGHT	39,760 LBS
DUNNAGE WEIGHT	963 LBS
CARLOAD WEIGHT	40,723 LBS

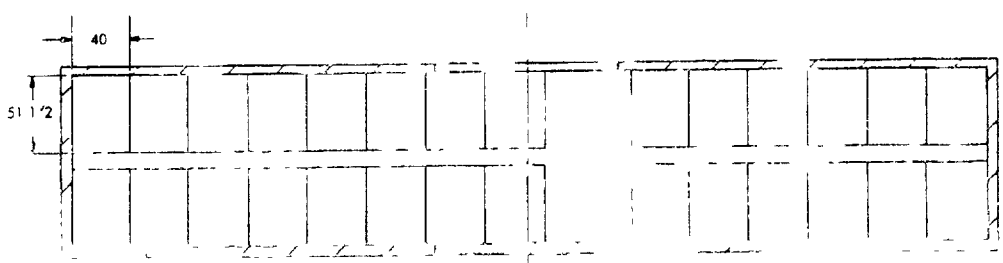

LOADING PLAN

Source: https://assist.dla.mil -- Downloaded: 2026-10-24T00:02Z
Check the source to verify that this is the current version before use.